


SITE PLAN

Skala 1 : 100

NOTE

INSTITUTION

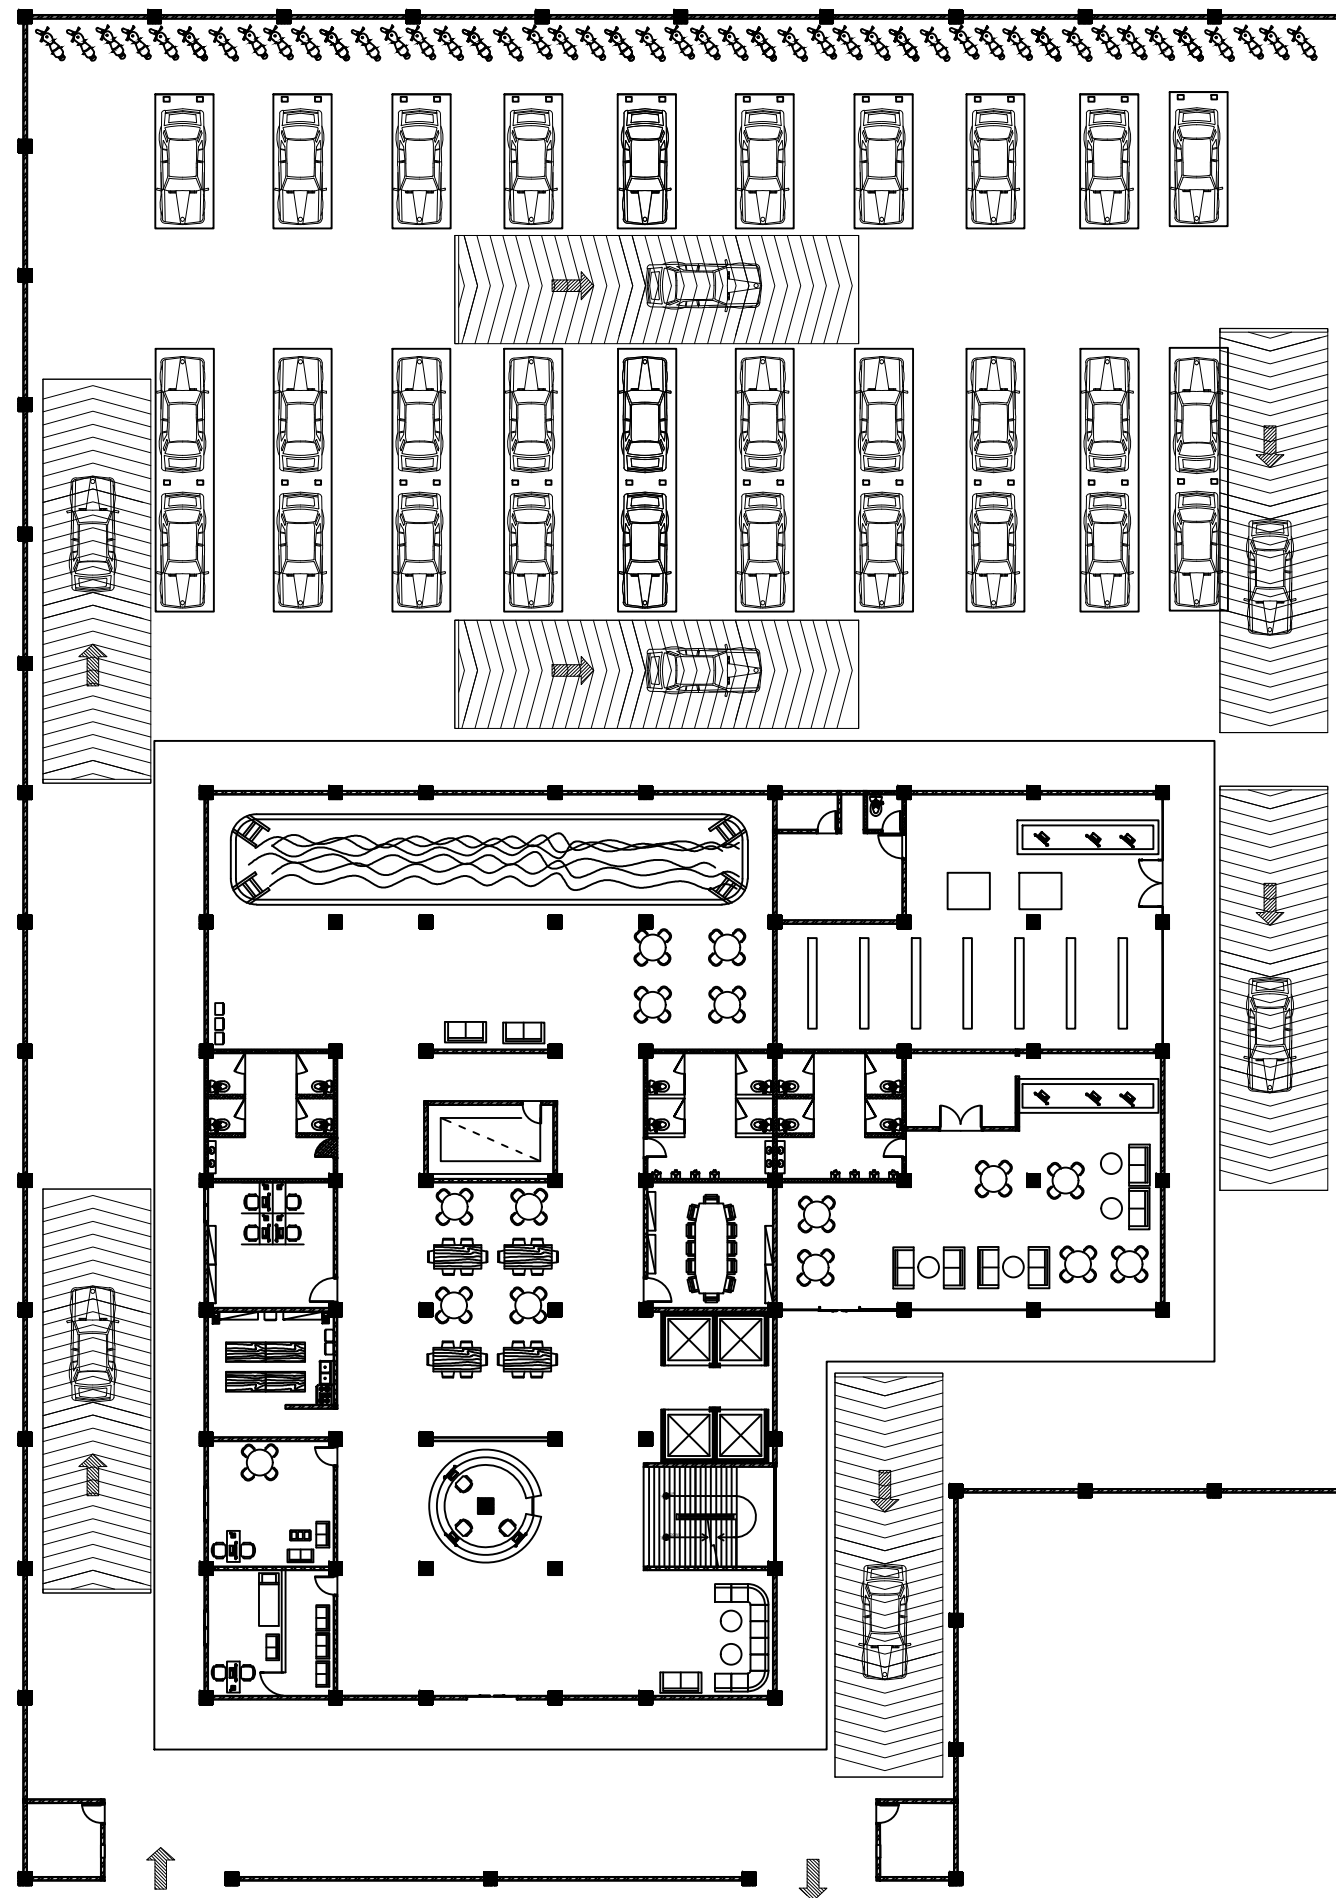

FACULTY OF ENGINEERING
UNIVERSITY SWADAYA GUNUNG
JATI CIREBON

TASK NAME

FINAL SEMESTER ASSIGNMENT

PROFESSION PLANNING
AND DESIGN
HIGH RISE BUILDING

MADE AS A FINAL SEMESTER
EXAMINATION ASSIGNMENT SCHOOL
YEAR 2020

LECTURER

INITIALS

Dr. SAIHUL ANWAR,Ir., M.Eng., MM.
NIDN. 417085401

DRAWN BY

INITIALS

MUHAMMAD NAZMI F
NPM. 120130085



IMAGE TITLE

HOTEL BUILDING
PLANNING WORK

IMAGE NAME

SITE PLAN

DATE	SCALE	DRAWING NUMBER	REVISION
03 FEBUARY 2021	1 : 100	01	-

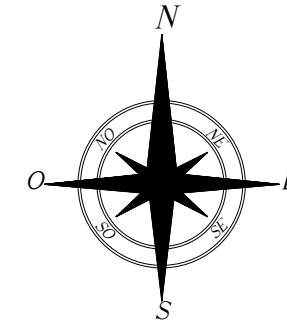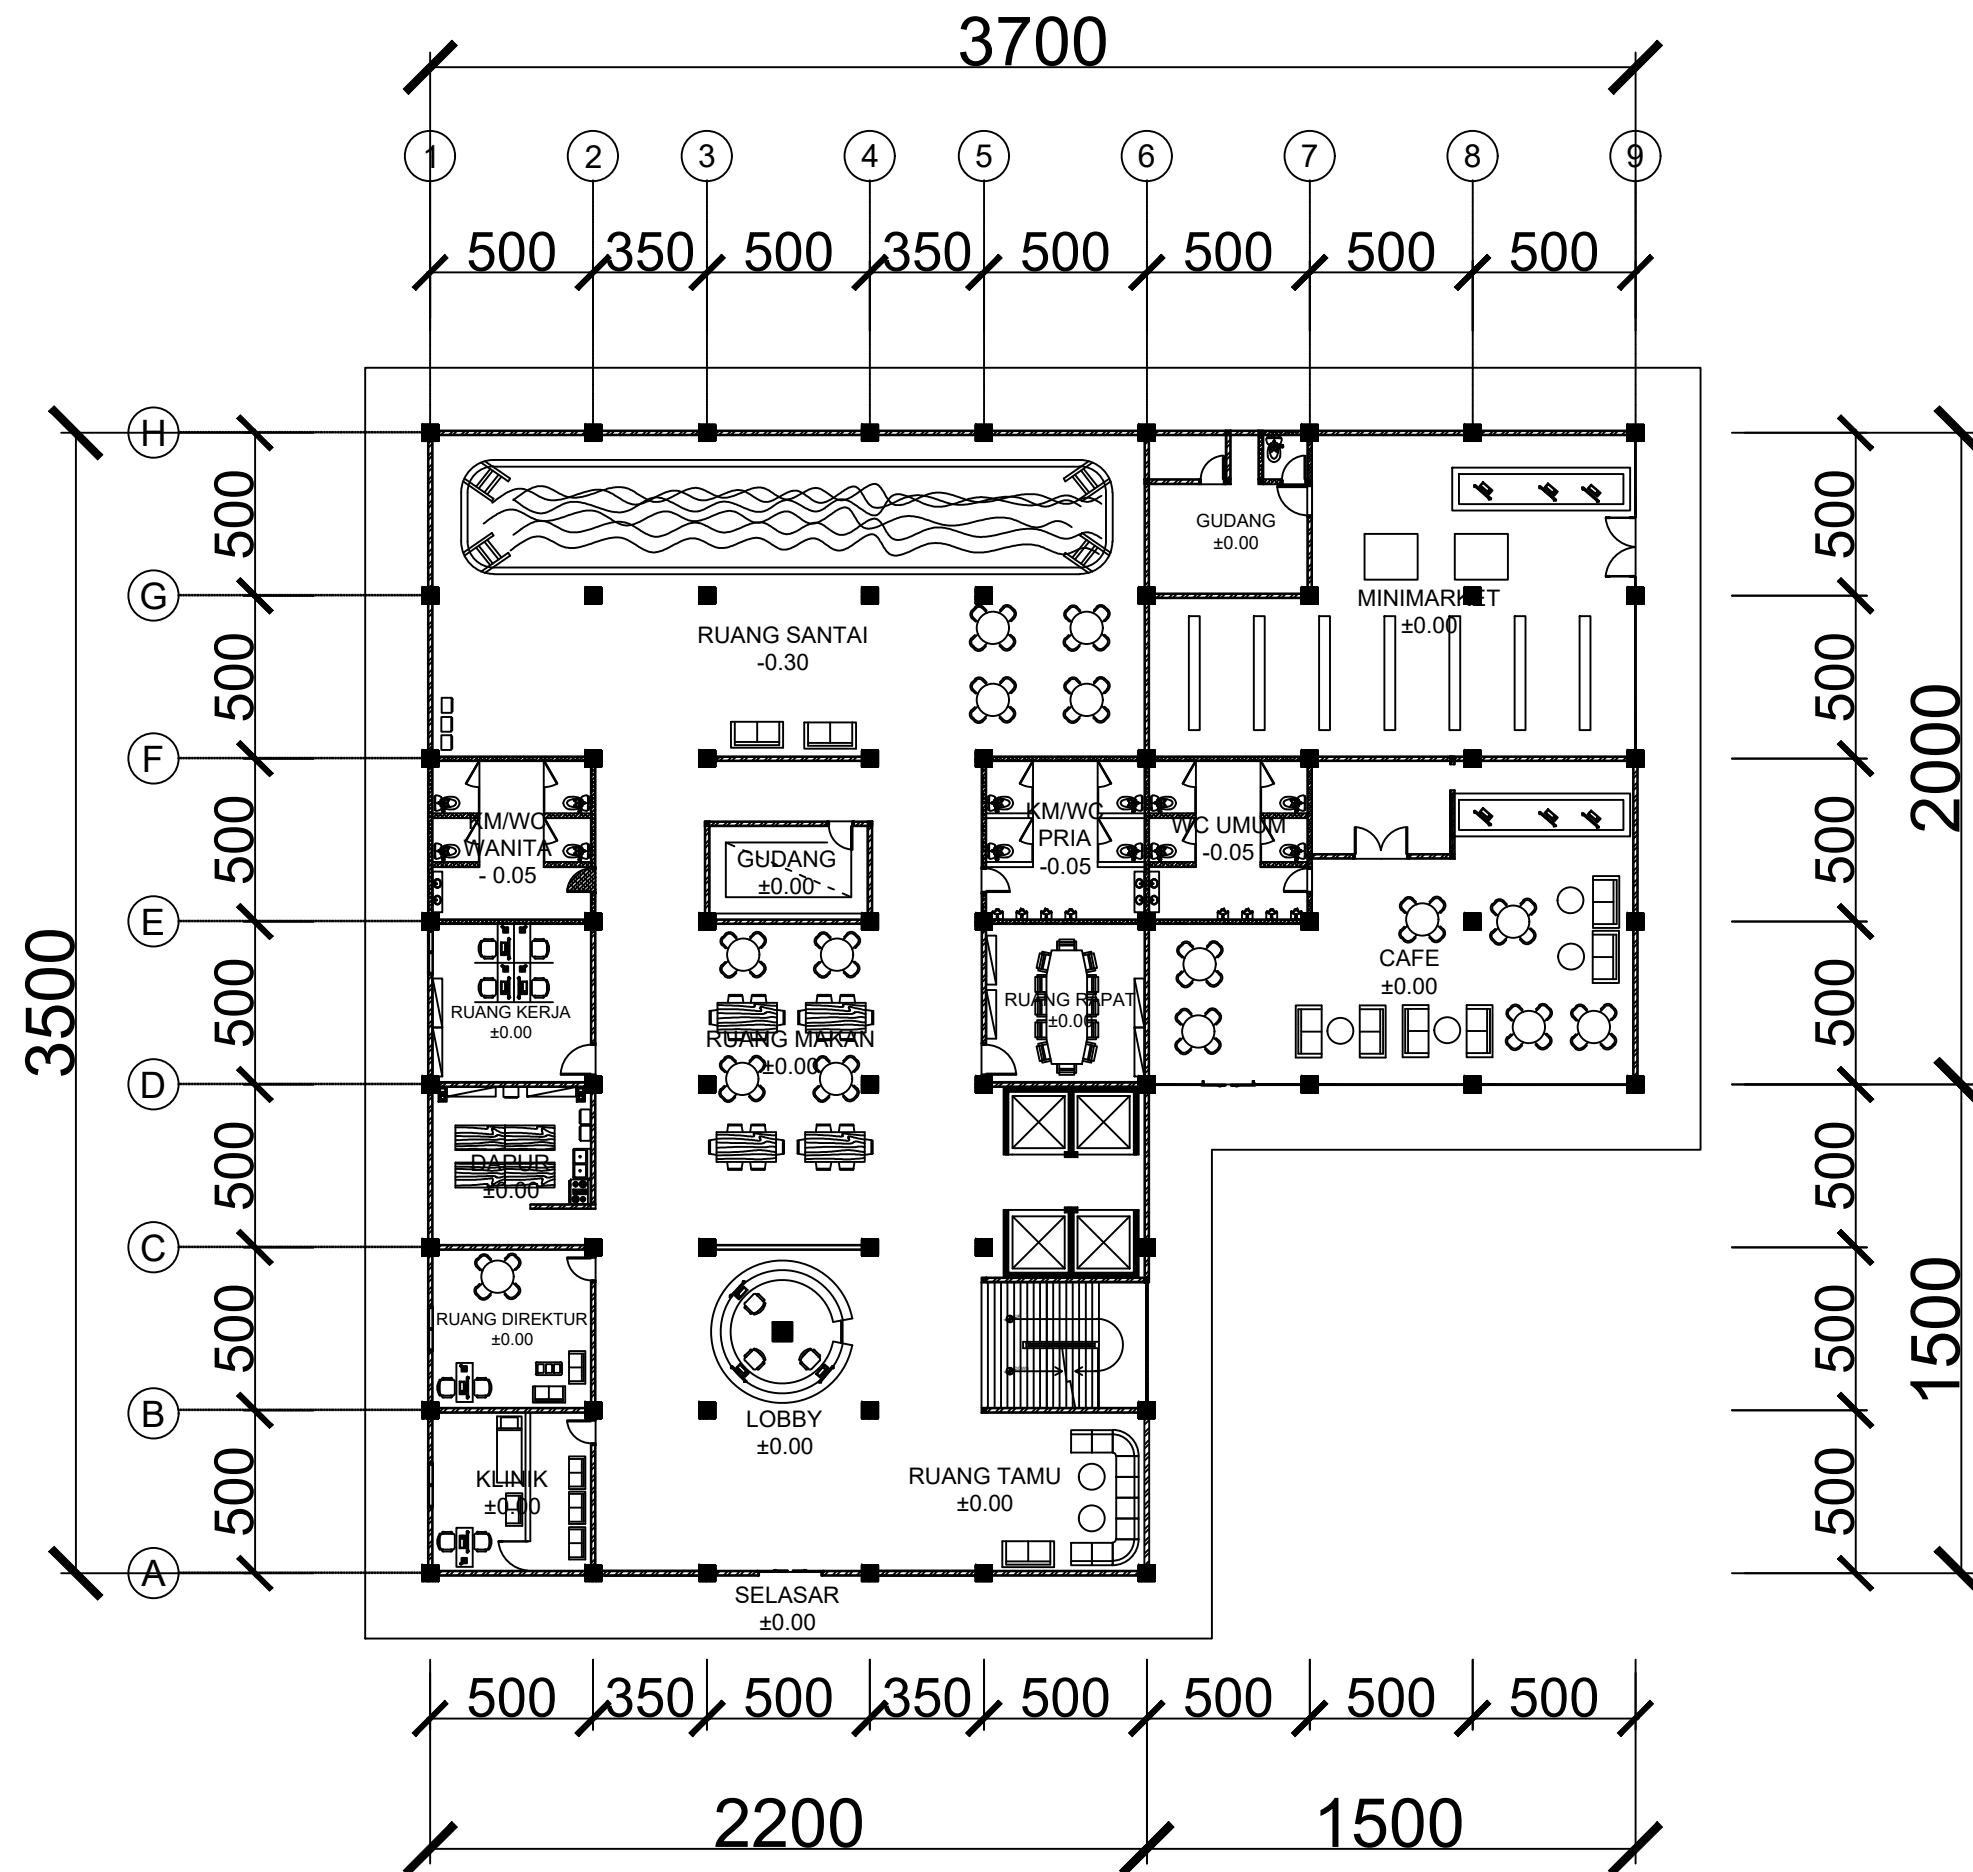

NOTE

INSTITUTION



FACULTY OF ENGINEERING
UNIVERSITY SWADAYA GUNUNG
JATI CIREBON

TASK NAME

FINAL SEMESTER ASSIGNMENT

PROFESSION PLANNING
AND DESIGN
HIGH RISE BUILDING

MADE AS A FINAL SEMESTER
EXAMINATION ASSIGNMENT SCHOOL
YEAR 2020

LECTURER

Dr. SAIHUL ANWAR, Ir., M.Eng., MM.
NIDN. 417085401

DRAWN BY

MUHAMMAD NAZMI F
NPM. 120130085



IMAGE TITLE

HOTEL BUILDING
PLANNING WORK

IMAGE NAME

1st FLOOR PLAN OF
HOTEL

DATE	SCALE	DRAWING NUMBER	REVISION
03 FEBUARY 2021	1 : 100	02	-

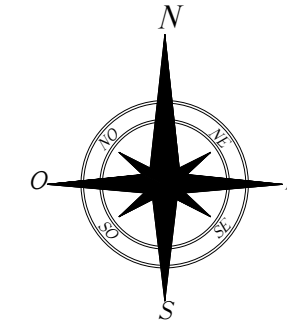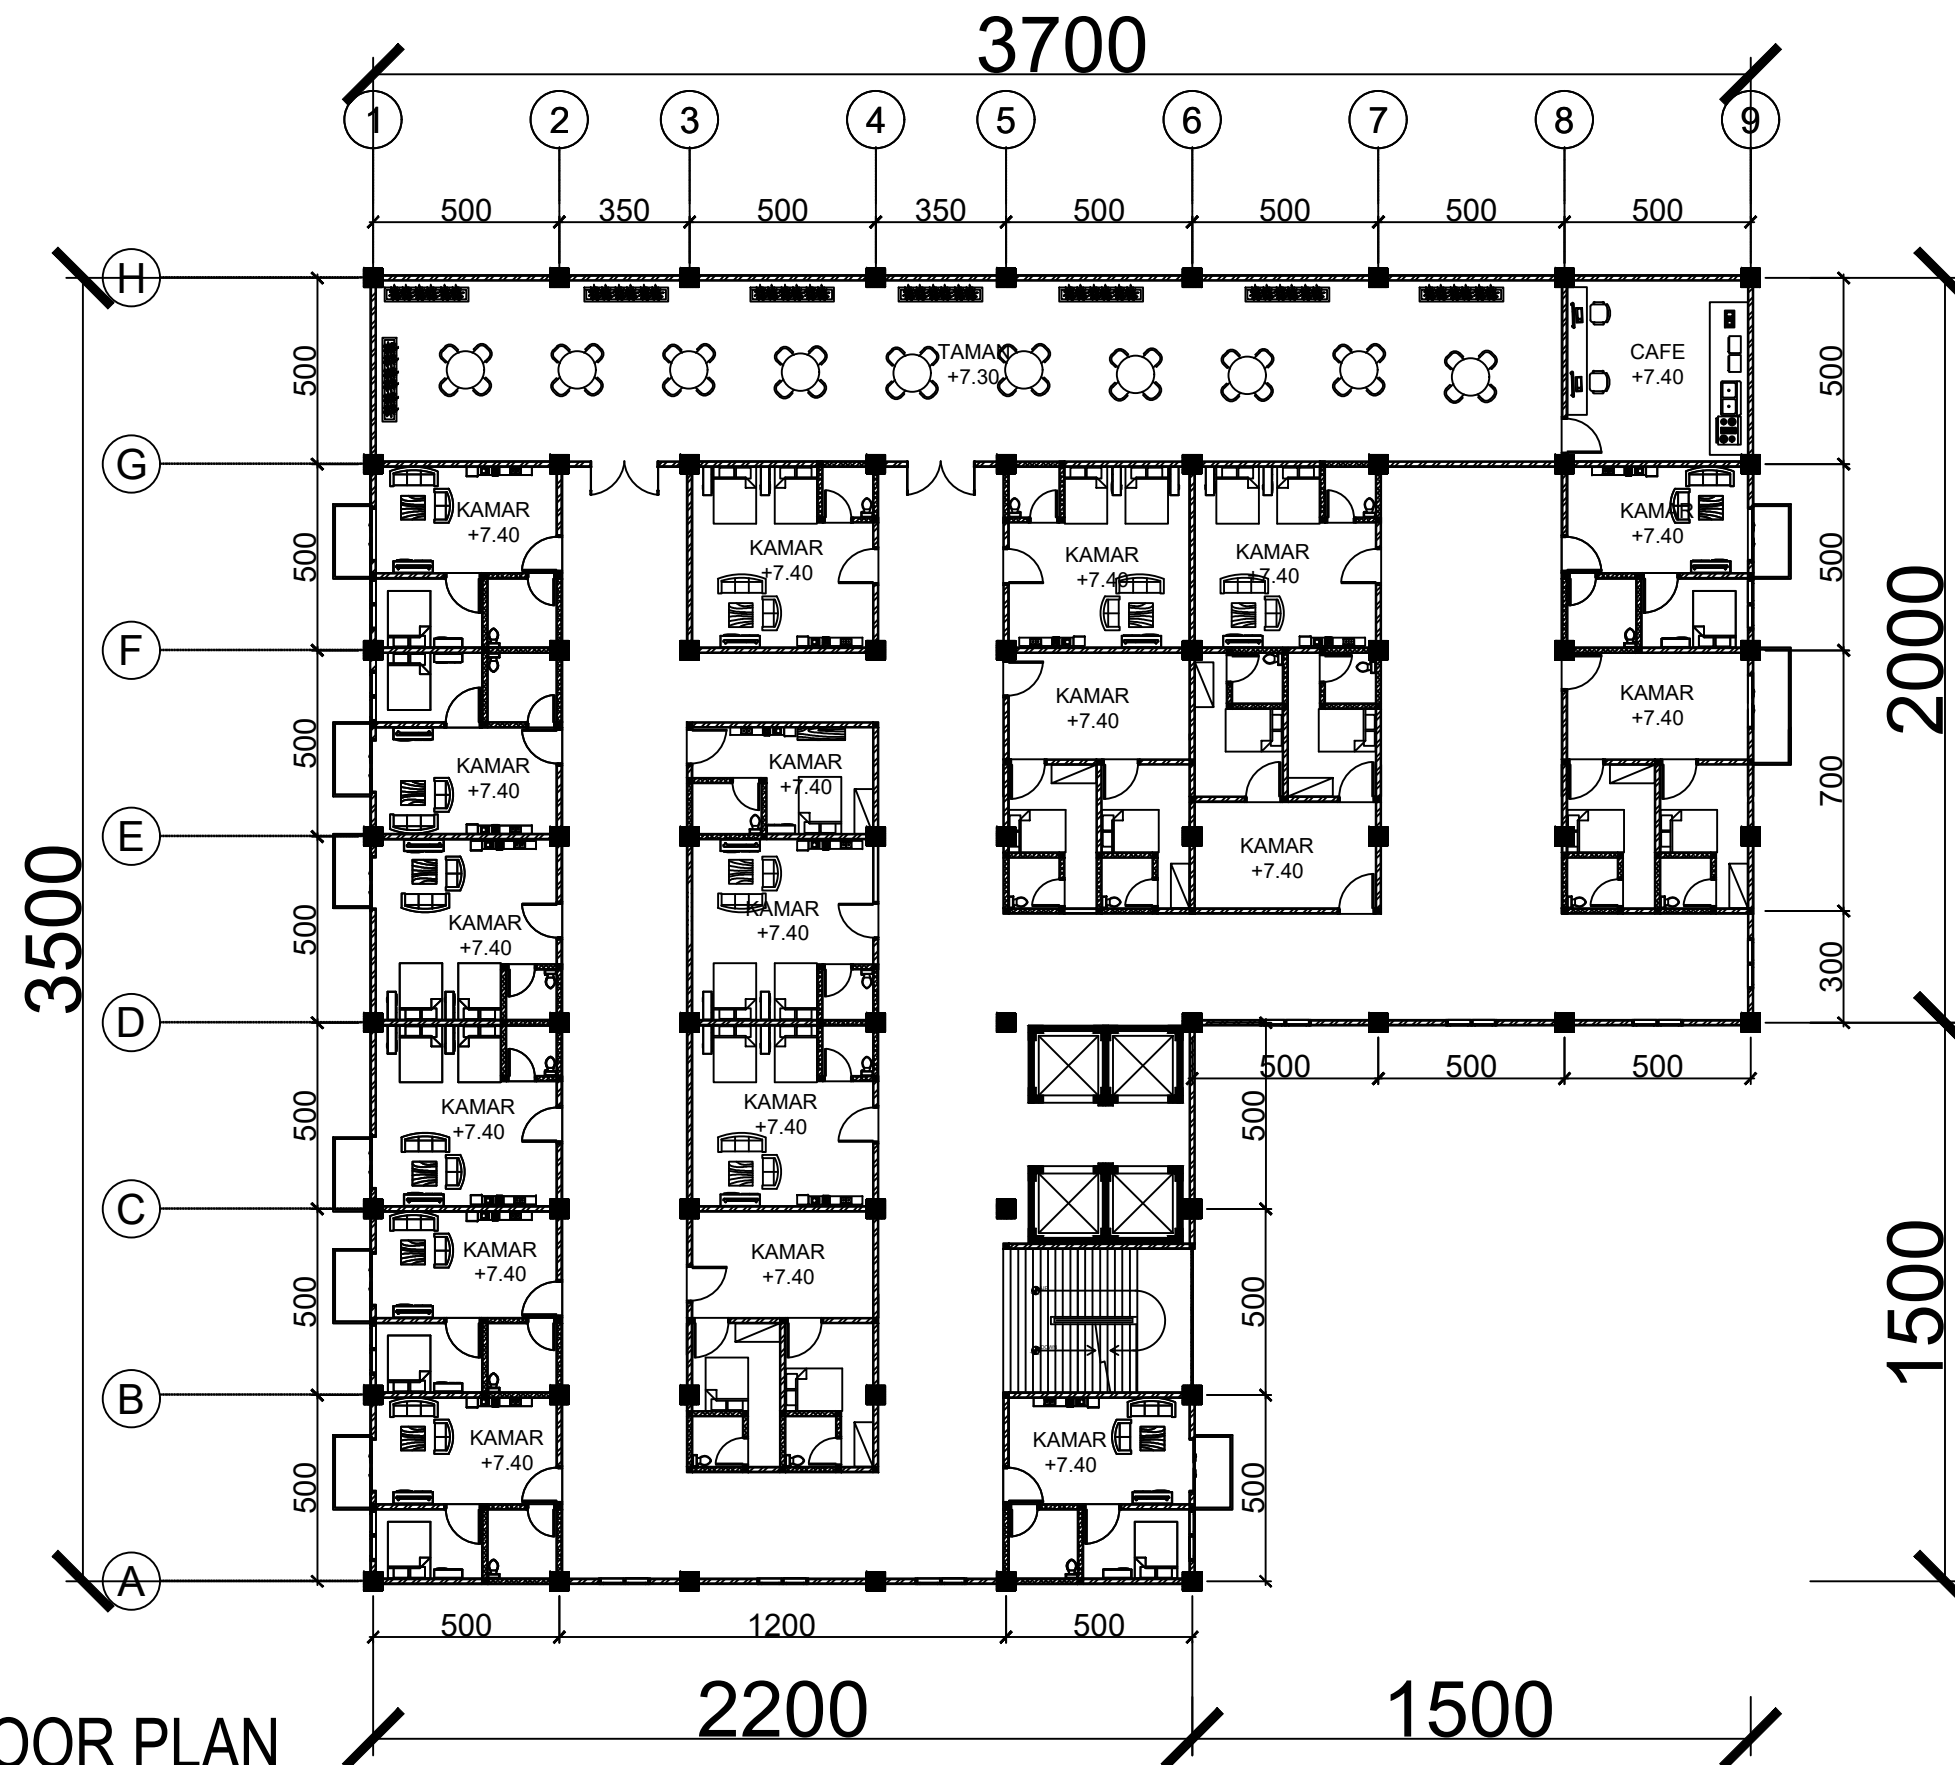

3rd FLOOR PLAN

Skala 1 : 100

NOTE

INSTITUTION



FACULTY OF ENGINEERING
UNIVERSITY SWADAYA GUNUNG
JATI CIREBON

TASK NAME

FINAL SEMESTER ASSIGNMENT

PROFESSION PLANNING
AND DESIGN
HIGH RISE BUILDING

MADE AS A FINAL SEMESTER
EXAMINATION ASSIGNMENT SCHOOL
YEAR 2020

LECTURER

Dr. SAIHUL ANWAR, Ir., M.Eng., MM.
NIDN. 417085401

DRAWN BY

MUHAMMAD NAZMI F
NPM. 120130085





IMAGE TITLE

HOTEL BUILDING
PLANNING WORK

IMAGE NAME

3rd FLOOR PLAN OF HOTEL

DATE	SCALE	DRAWING NUMBER	REVISION
03 FEBUARY 2021	1 : 100	04	-

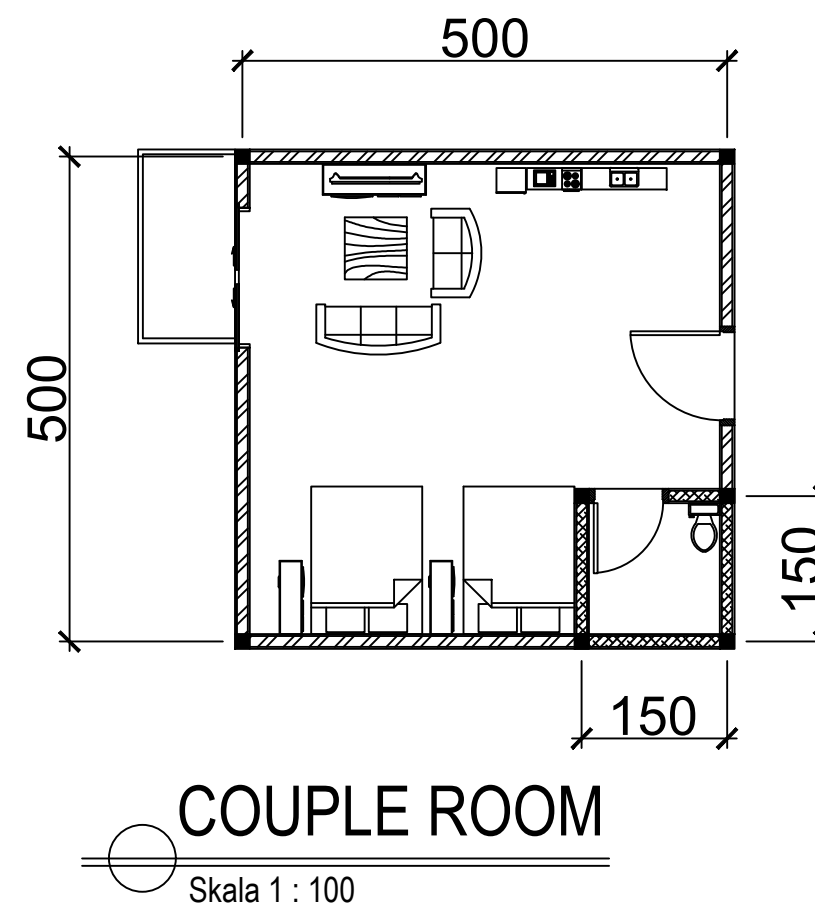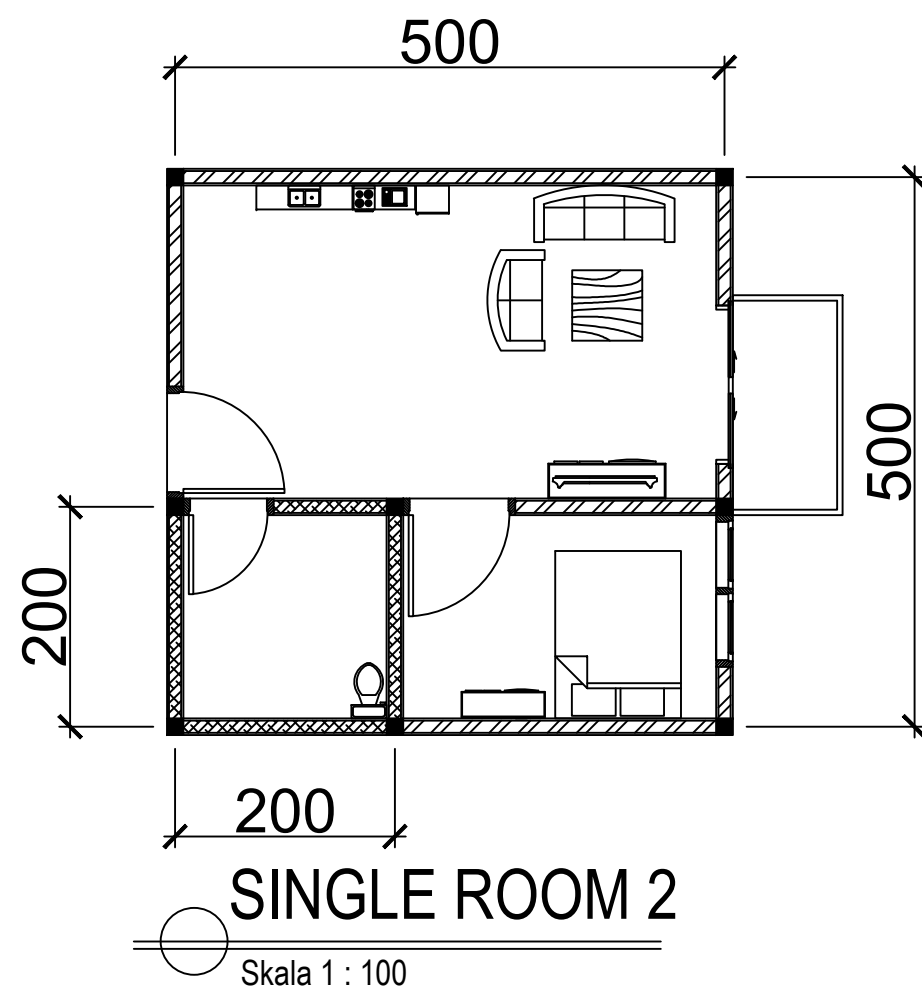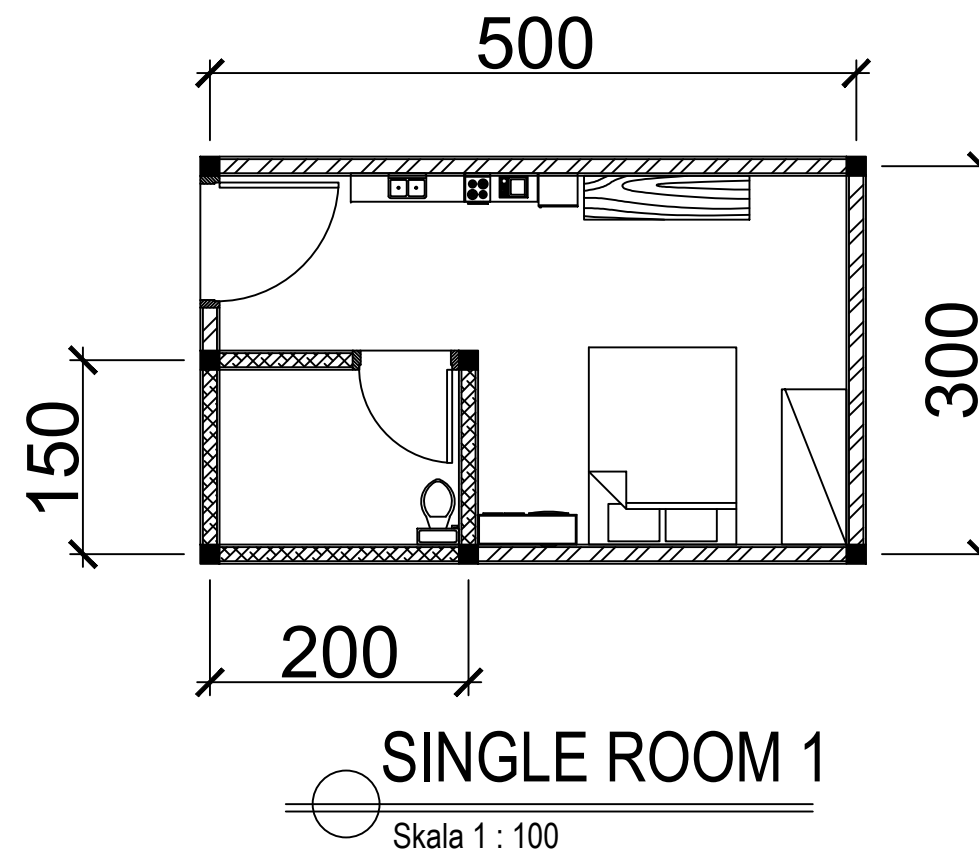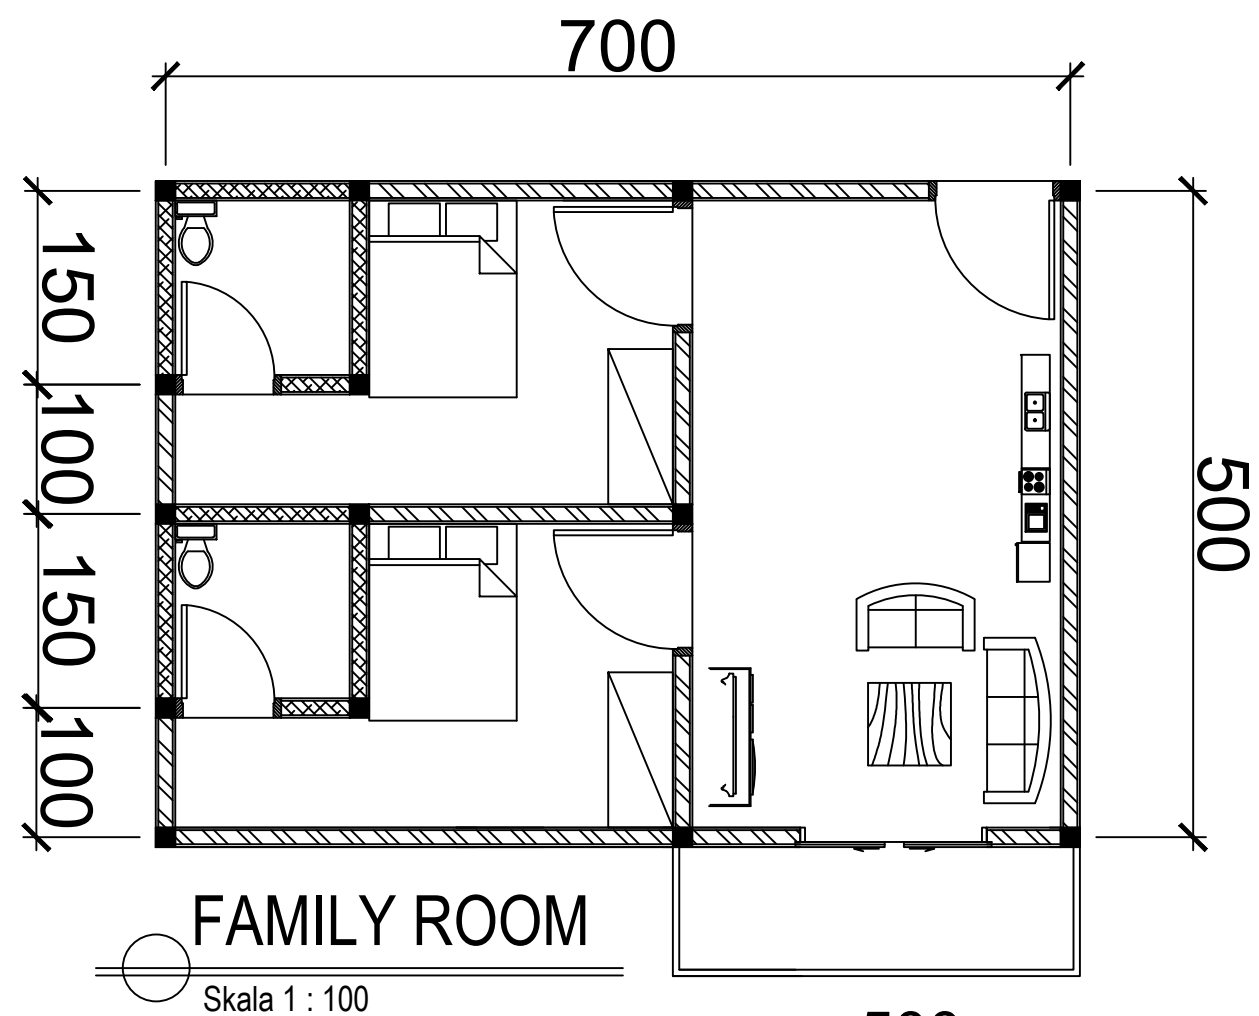

NOTE

INSTITUTION



FACULTY OF ENGINEERING
UNIVERSITY SWADAYA GUNUNG
JATI CIREBON

TASK NAME

FINAL SEMESTER ASSIGNMENT

PROFESSION PLANNING
AND DESIGN
HIGH RISE BUILDING

MADE AS A FINAL SEMESTER
EXAMINATION ASSIGNMENT SCHOOL
YEAR 2020

LECTURER

Dr. SAIHUL ANWAR,Ir., M.Eng., MM.
NIDN. 417085401

DRAWN BY

MUHAMMAD NAZMI F
NPM. 120130085



IMAGE TITLE

HOTEL BUILDING
PLANNING WORK

IMAGE NAME

DETAIL ROOM

DATE	SCALE	DRAWING NUMBER	REVISION
03 FEBUARI 2021	1 : 100	06	-

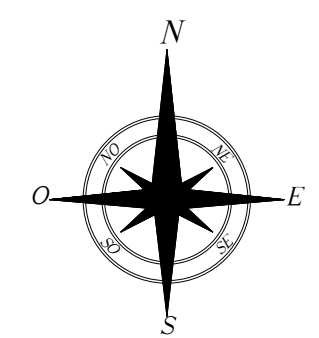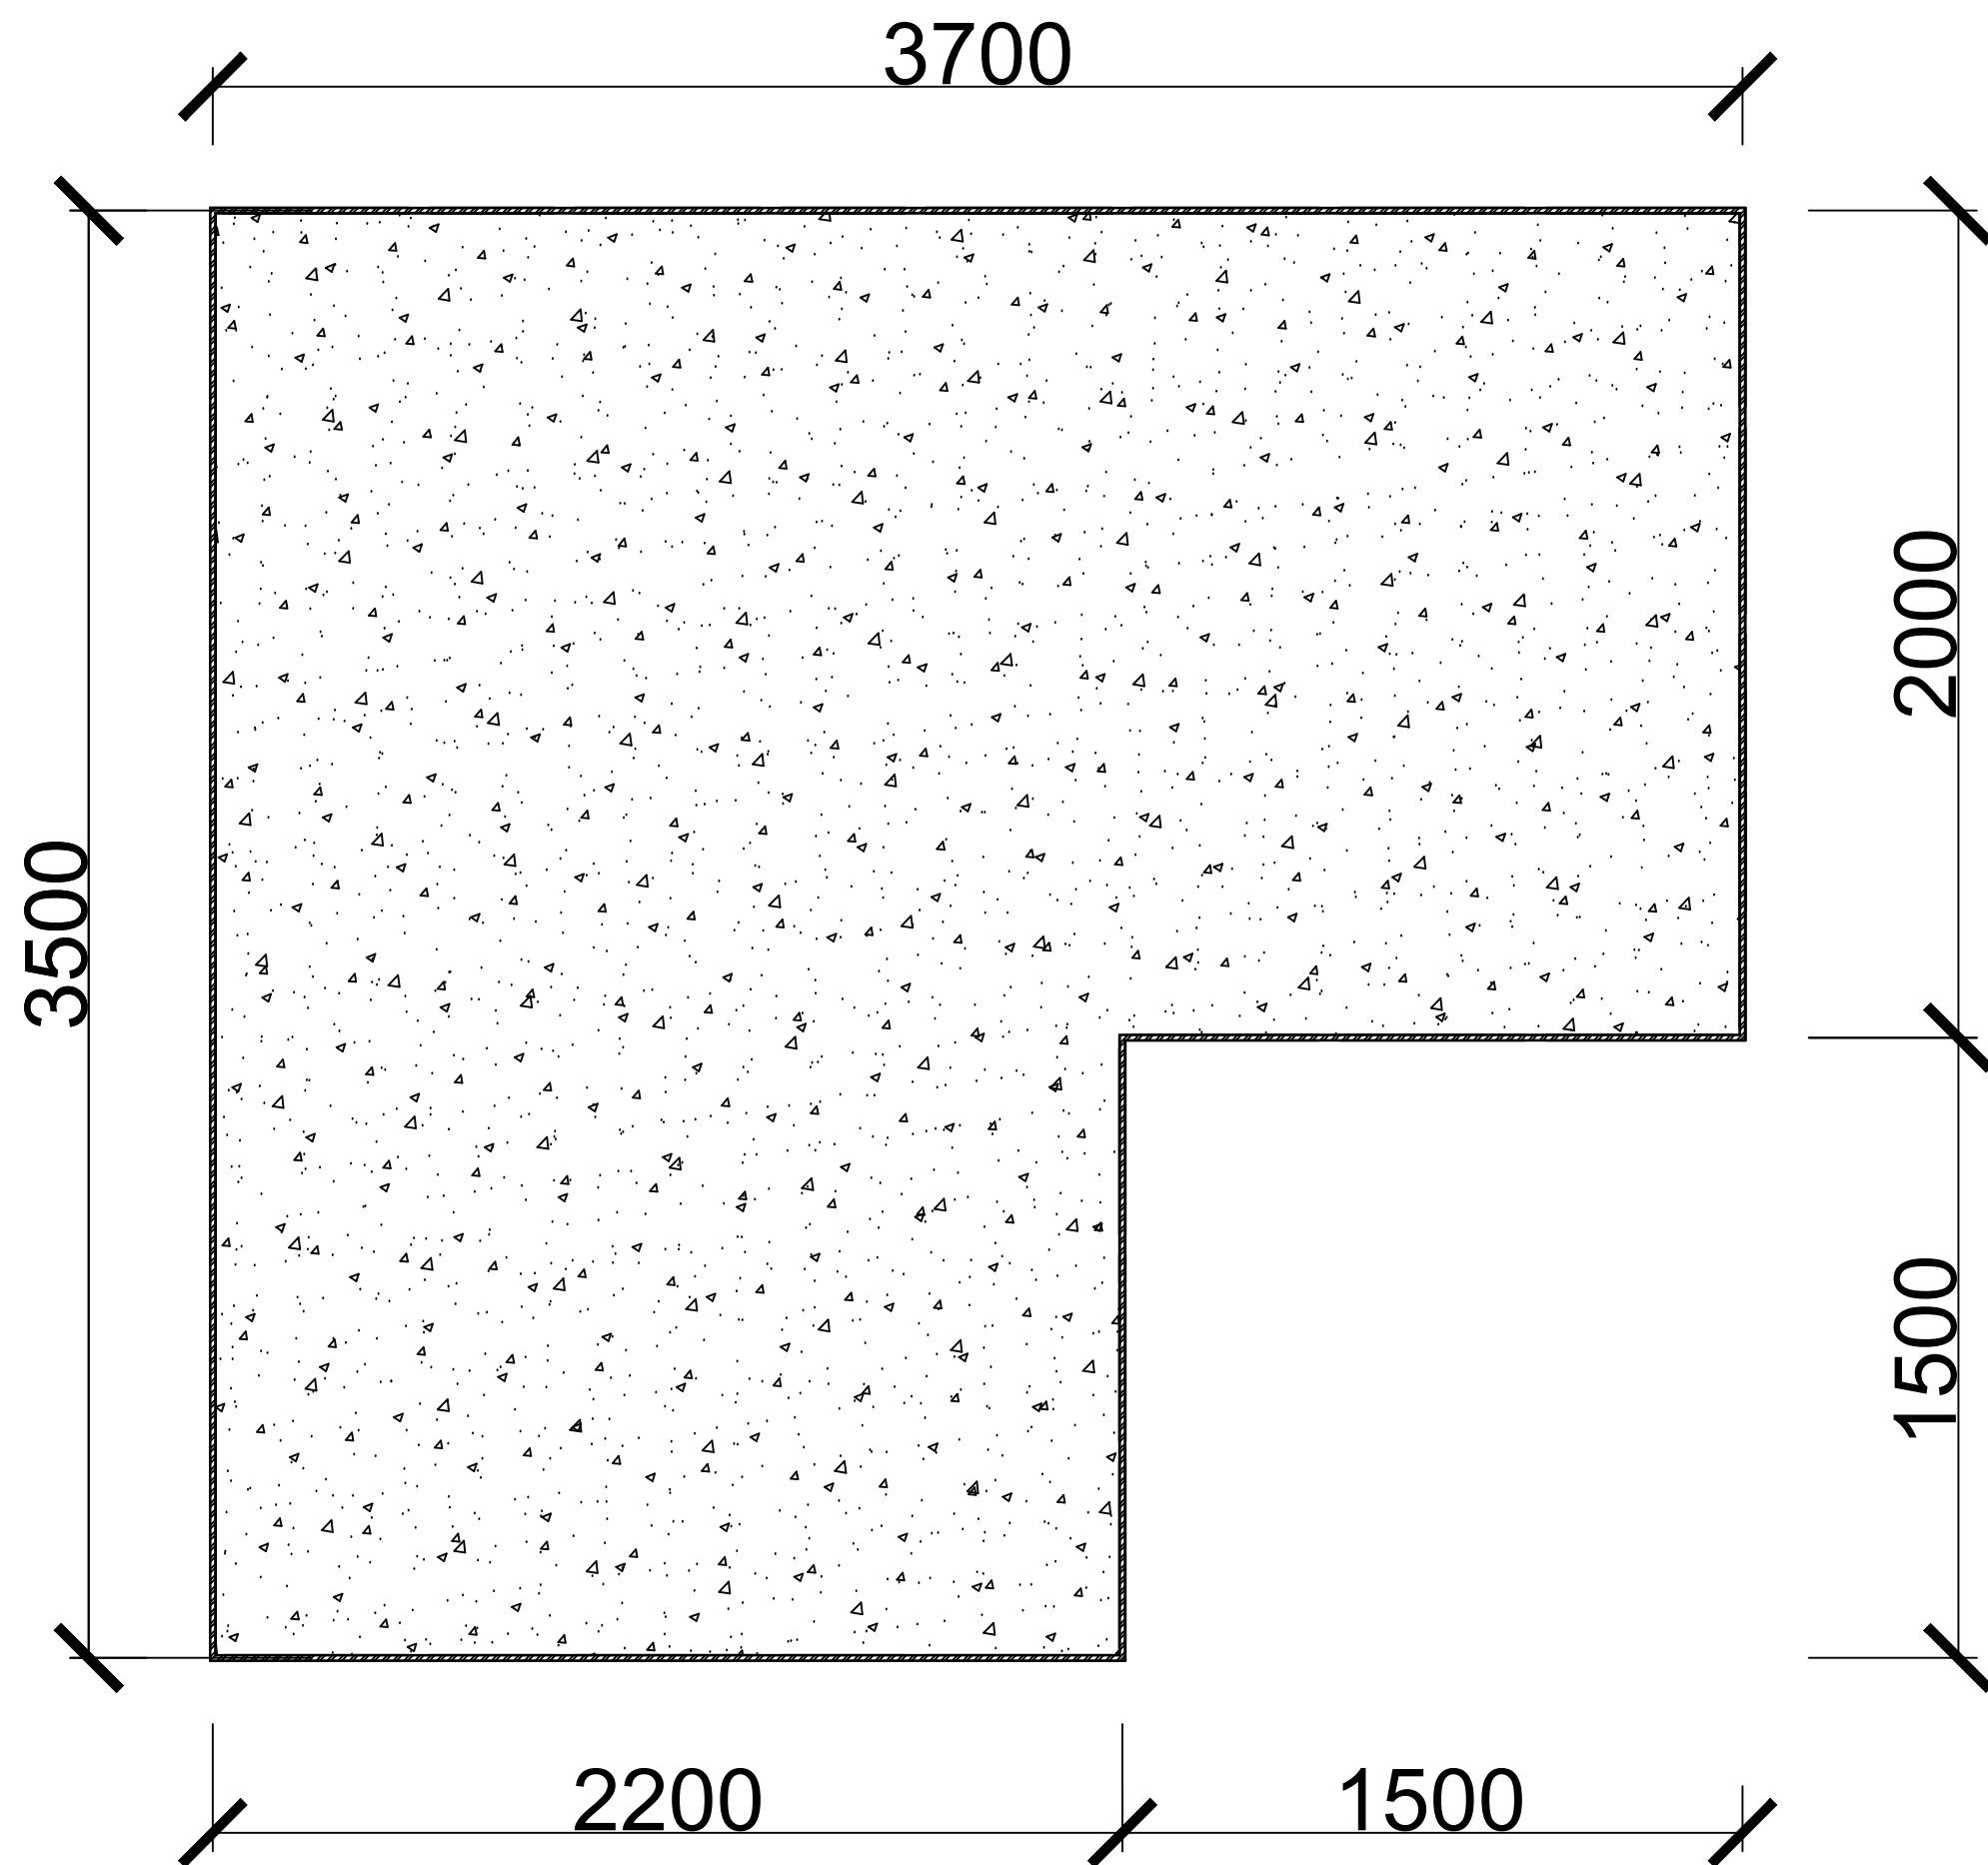

Roof plan

Skala 1 : 100

NOTE

INSTITUTION



FACULTY OF ENGINEERING
UNIVERSITY SWADAYA GUNUNG
JATI CIREBON

TASK NAME

FINAL SEMESTER ASSIGNMENT

PROFESSION PLANNING
AND DESIGN
HIGH RISE BUILDING

MADE AS A FINAL SEMESTER
EXAMINATION ASSIGMENT SCHOOL
YEAR 2020

LECTURER

INITIALS

Dr. SAIHUL ANWAR,Ir., M.Eng., MM.
NIDN. 417085401

DRAWN BY

INITIALS

MUHAMMAD NAZMI F
NPM. 120130085



IMAGE TITLE

HOTEL BUILDING
PLANNING WORK

IMAGE NAME



ROOF PLAN OF HOTEL

DATE	SCALE	DRAWING NUMBER	REVISION
03 FEBUARY 2021	1 : 100	07	-

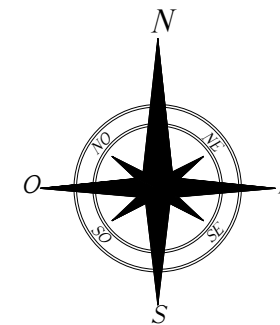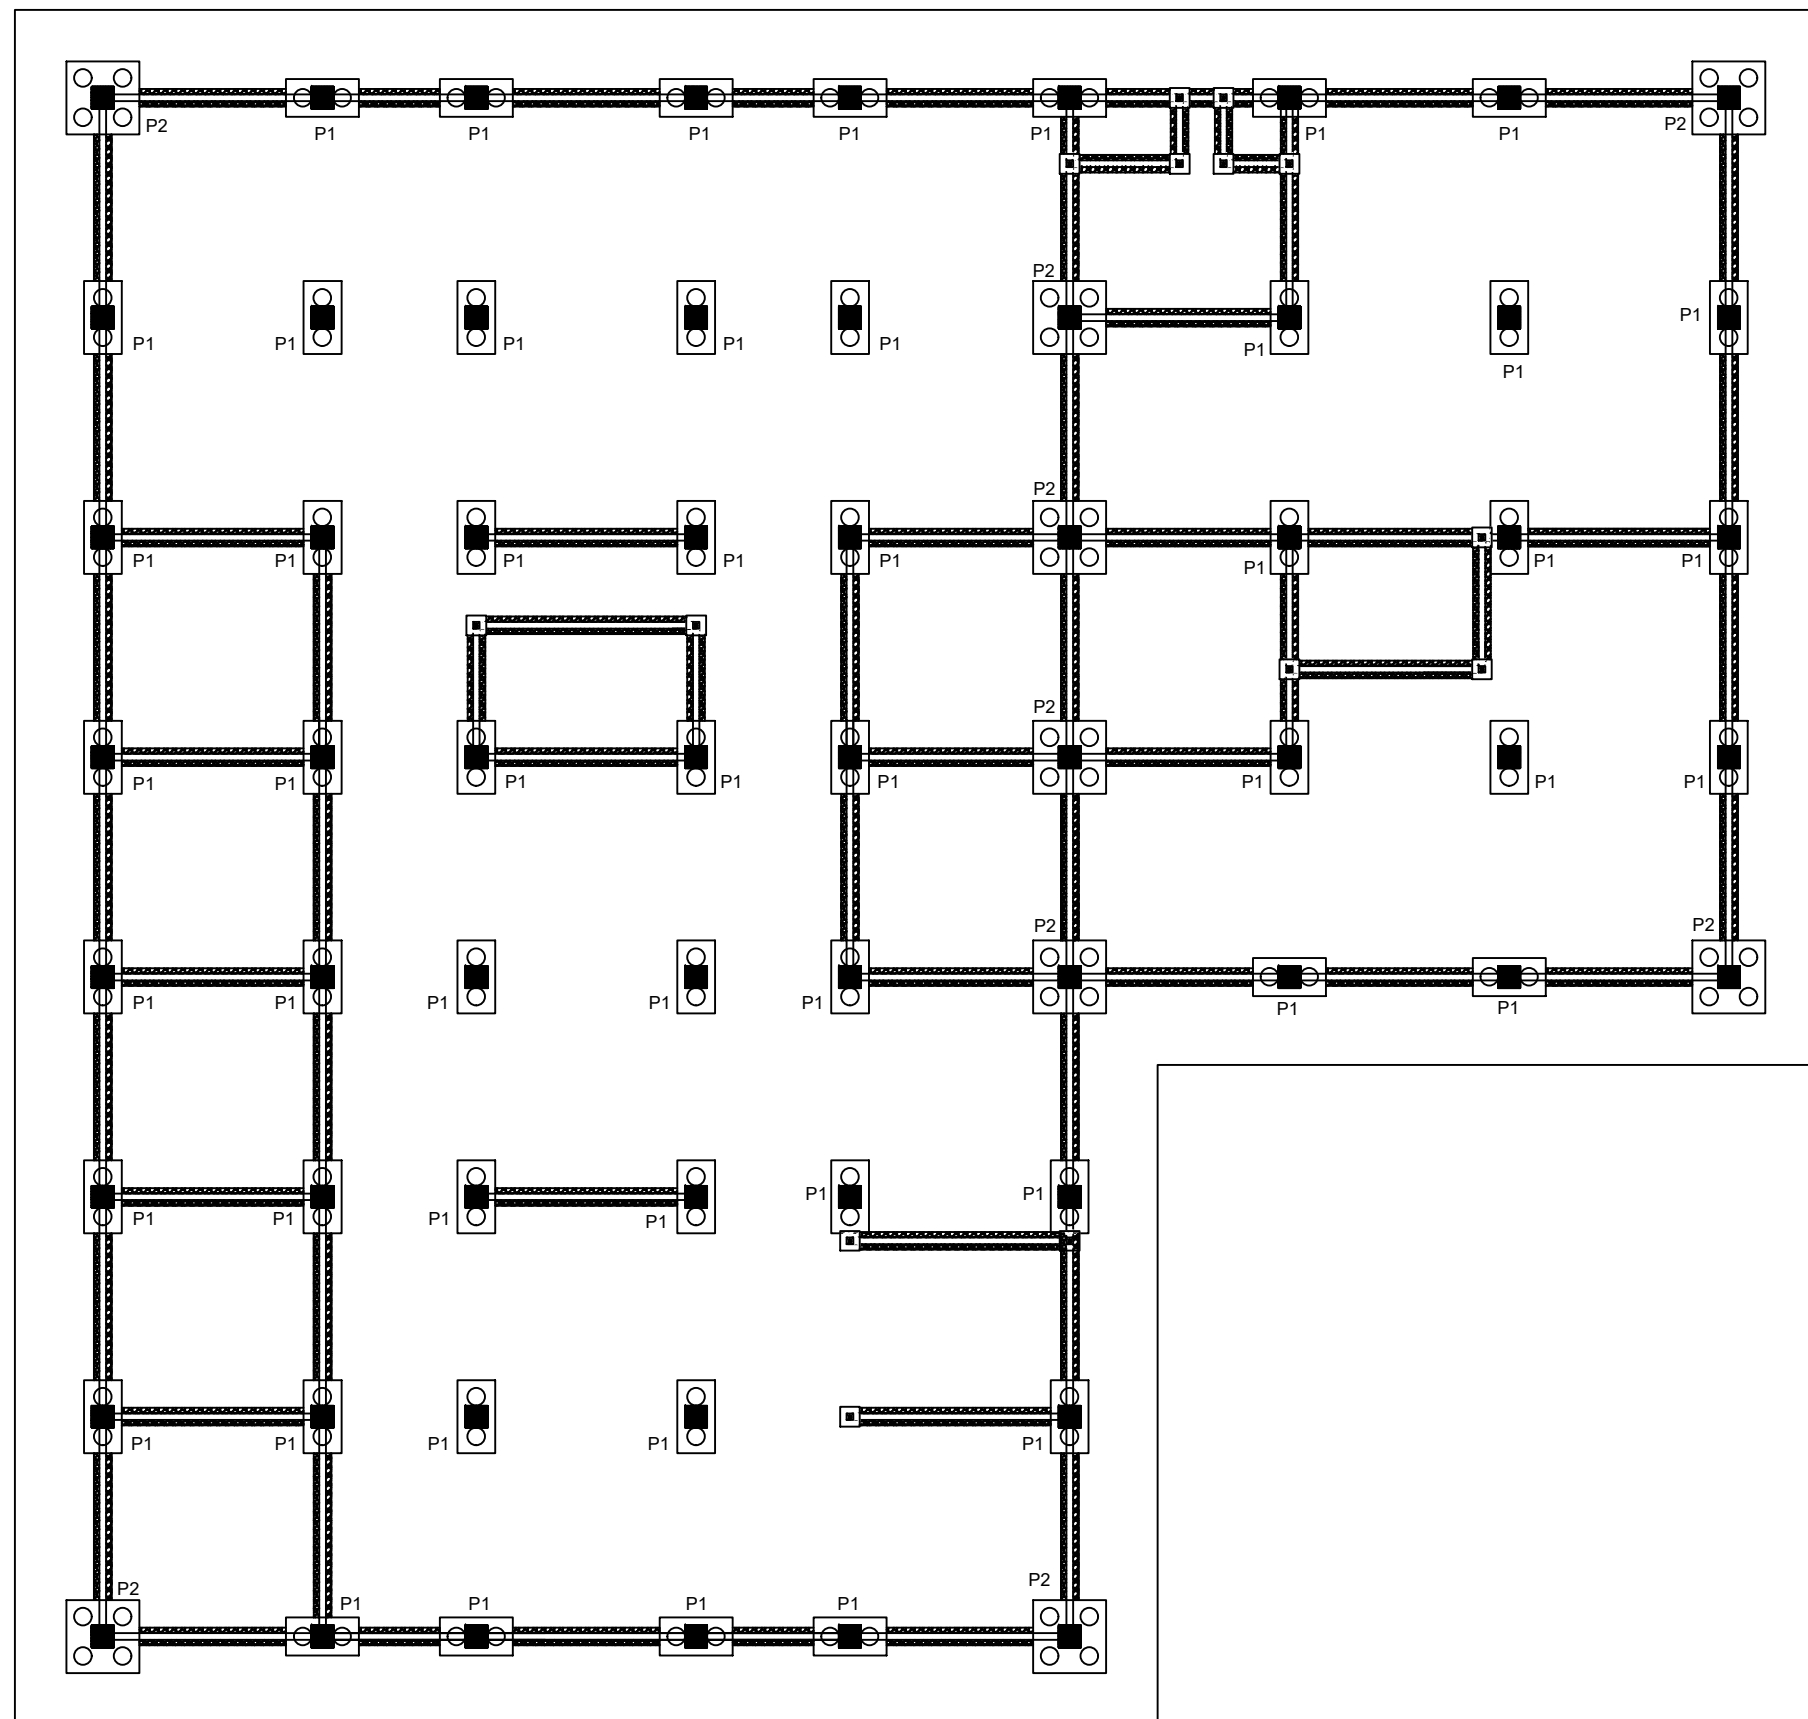

NOTE

KETERANGAN
PONDASI
P1=2 TIANG PANCANG Ø 400mm p=16 M
P2=4 TIANG PANCANG Ø 400mm p=16 M

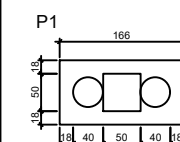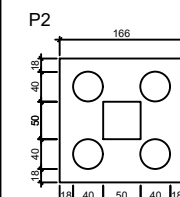

INSTITUTION



FACULTY OF ENGINEERING
UNIVERSITY SWADAYA GUNUNG
JATI CIREBON

TASK NAME

FINAL SEMESTER ASSIGNMENT

PROFESSION PLANNING
AND DESIGN
HIGH RISE BUILDING

MADE AS A FINAL SEMESTER
EXAMINATION ASSIGNMENT SCHOOL
YEAR 2020

LECTURER

INITIALS

Dr. SAIHUL ANWAR,Ir., M.Eng., MM.
NIDN. 417085401

DRAWN BY

INITIALS

MUHAMMAD NAZMI F
NPM. 120130085

IMAGE TITLE

HOTEL BUILDING
PLANNING WORK



IMAGE NAME

FOUNDATION PLAN OF HOTEL


DATE	SCALE	DRAWING NUMBER	REVISION
03 FEBUARY 2021	1 : 100	08	-

FOUNDATION PLAN


Skala 1 : 100

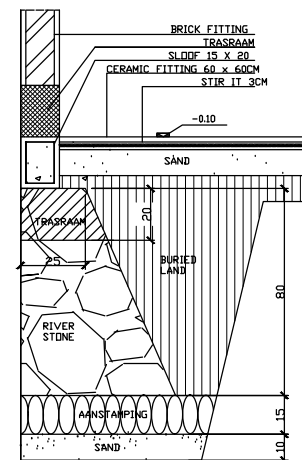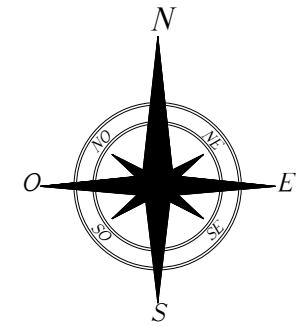


FOUNDATION DETAIL PIECES A
SCALE 1:20

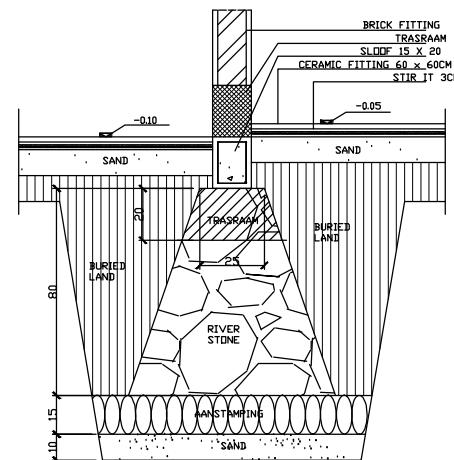

FOUNDATION DETAIL PIECES B
SCALE 1:20

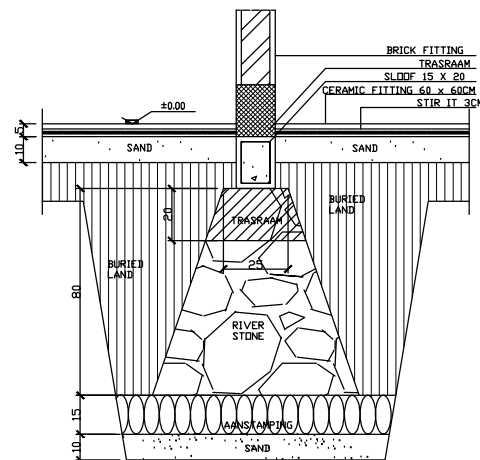

FOUNDATION DETAIL PIECES C
SCALE 1:20

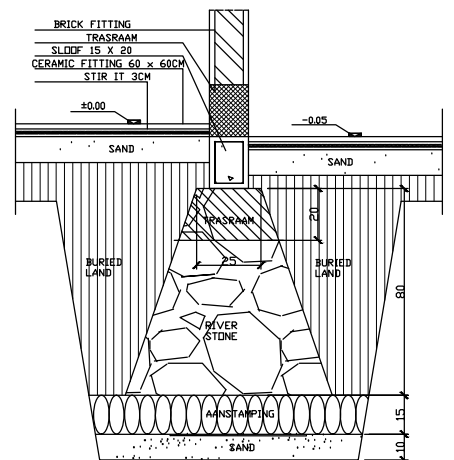

FOUNDATION DETAIL PIECES D
SCALE 1:20

RIVER FOUNDATION DETAILS

Scale 1 : 20

NOTE

INSTITUTION



FACULTY OF ENGINEERING
UNIVERSITY SWADAYA GUNUNG
JATI CIREBON

TASK NAME

FINAL SEMESTER ASSIGNMENT

PROFESSION PLANNING
AND DESIGN
HIGH RISE BUILDING

MADE AS A FINAL SEMESTER
EXAMINATION ASSIGMENT SCHOOL
YEAR 2020

LECTURER

INITIALS

Dr. SAIHUL ANWAR,Ir., M.Eng., MM.
NIDN. 417085401

DRAWN BY

INITIALS

MUHAMMAD NAZMI F
NPM. 120130085

IMAGE TITLE



HOTEL BUILDING
PLANNING WORK

IMAGE NAME

RIVER FOUNDATION DETAILS

DATE	SCALE	DRAWING NUMBER	REVISION
03 FEBUARY 2021	1 : 20	09	-

P1

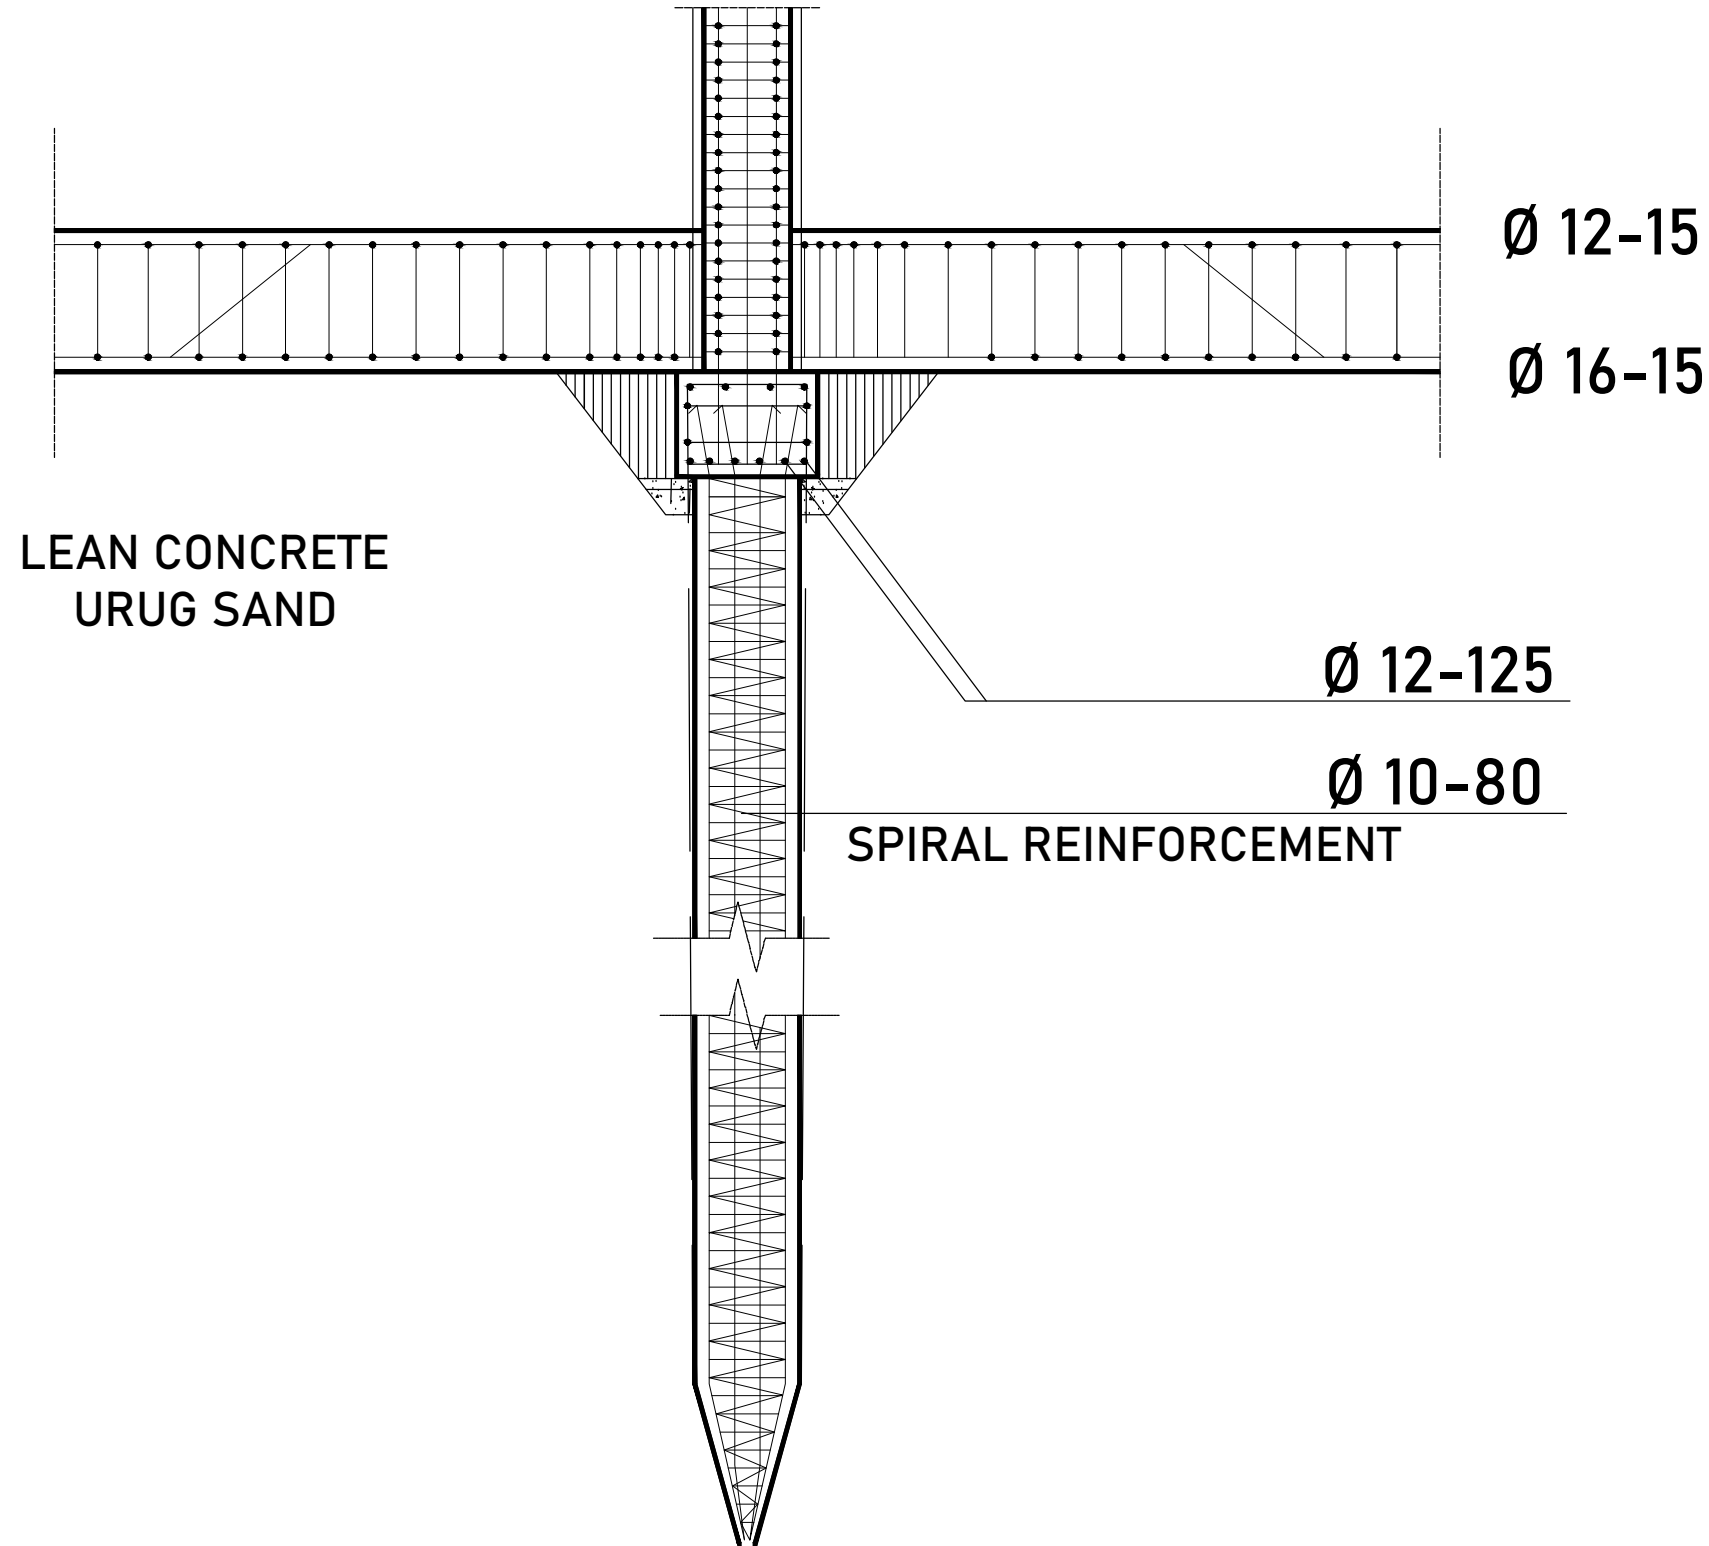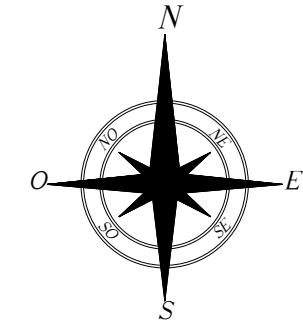

FOUNDATION PILE CAP DETAILS 1

Scale 1 : 20

NOTE

INSTITUTION



FACULTY OF ENGINEERING
UNIVERSITY SWADAYA GUNUNG
JATI CIREBON

TASK NAME

FINAL SEMESTER ASSIGNMENT

PROFESSION PLANNING
AND DESIGN
HIGH RISE BUILDING

MADE AS A FINAL SEMESTER
EXAMINATION ASSIGMENT SCHOOL
YEAR 2020

LECTURER

INITIALS

Dr. SAIHUL ANWAR,Ir., M.Eng., MM.
NIDN. 417085401

DRAWN BY

INITIALS

MUHAMMAD NAZMI F
NPM. 120130085




IMAGE TITLE

HOTEL BUILDING
PLANNING WORK

IMAGE NAME

FOUNDATION PILE CAP
DETAILS 1

DATE	SCALE	DRAWING NUMBER	REVISION
03 FEBUARY 2021	1 : 20	10	-

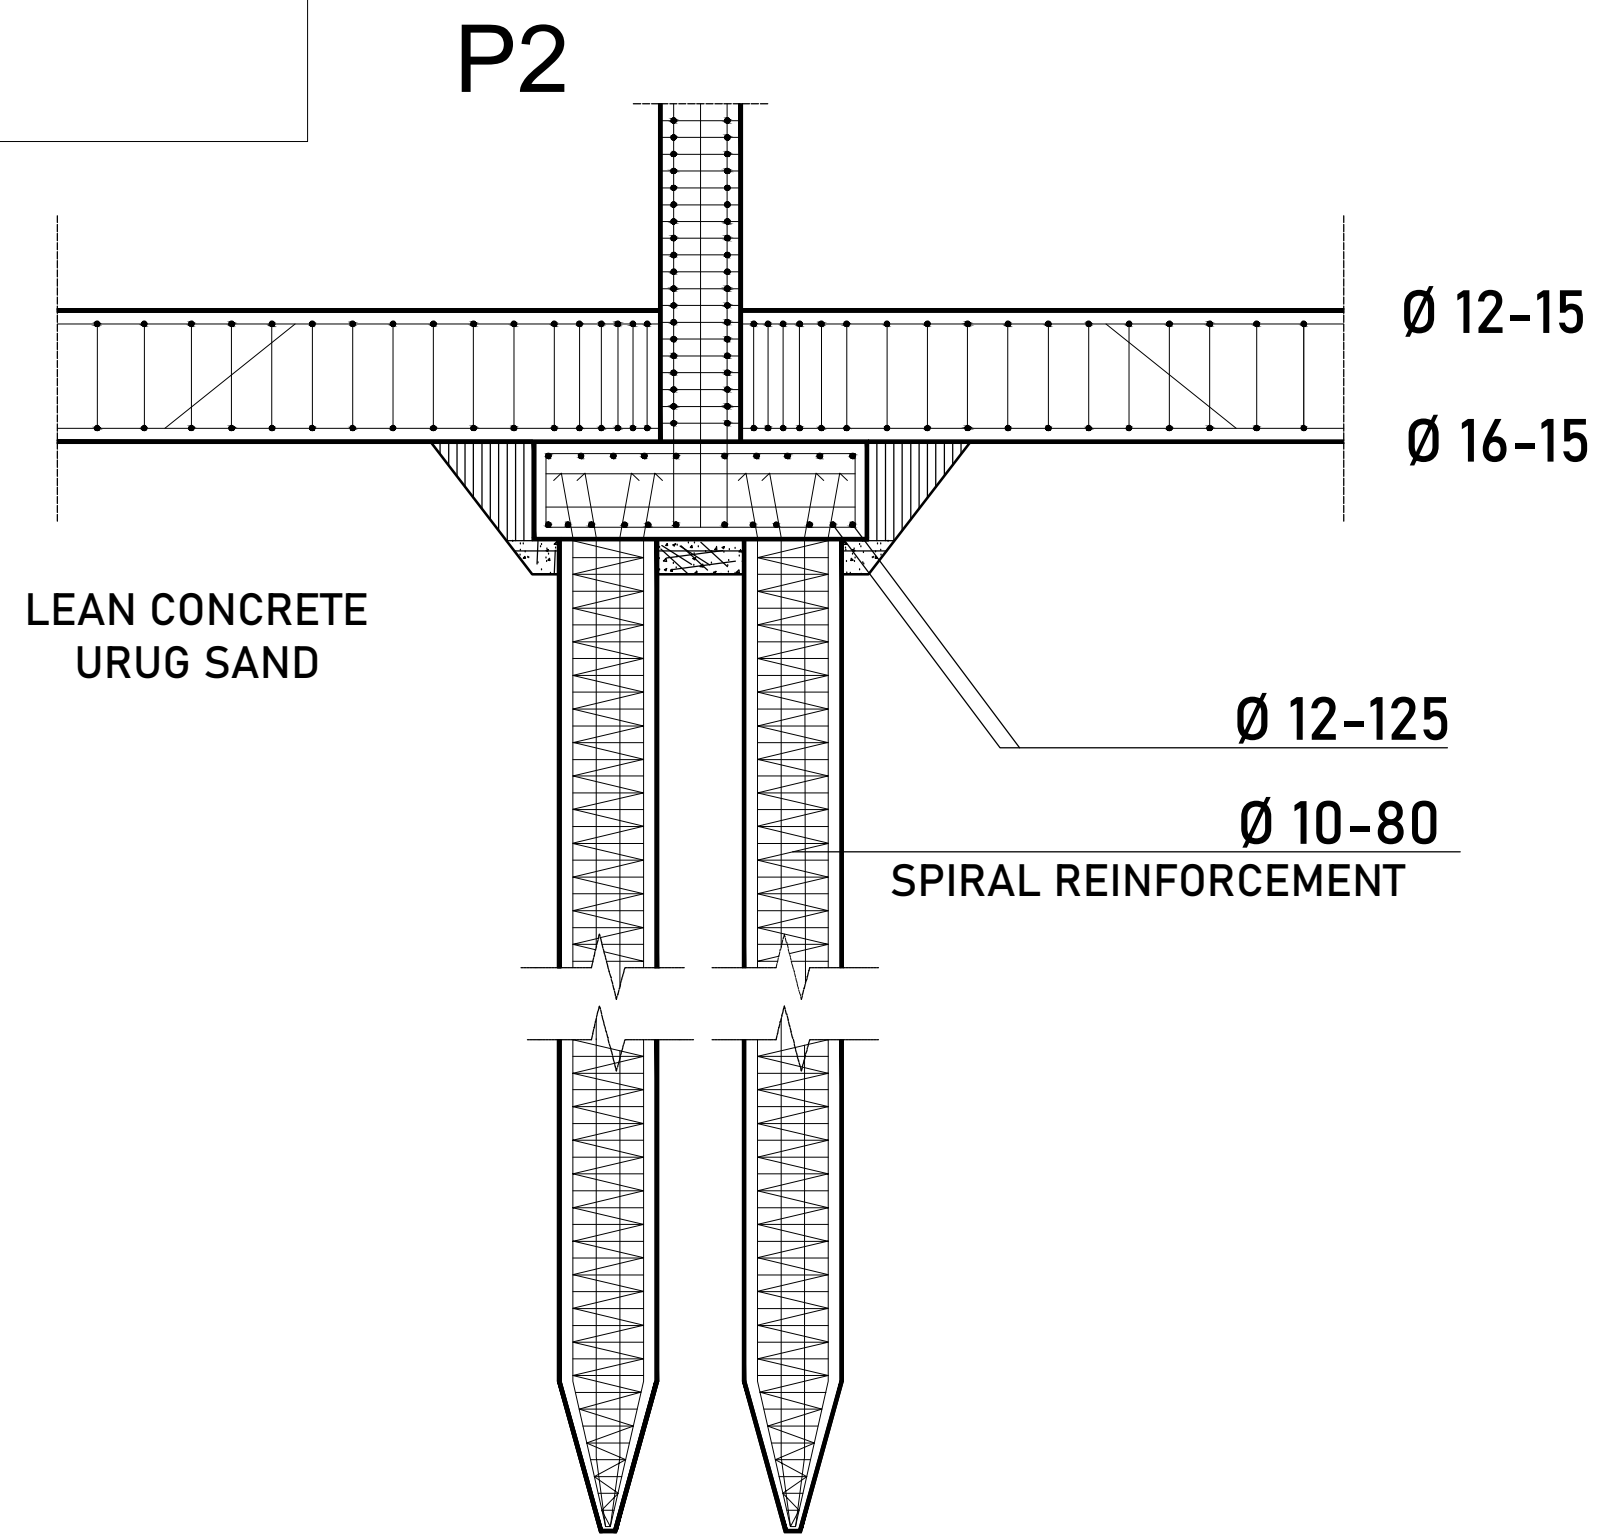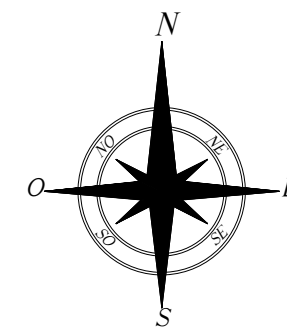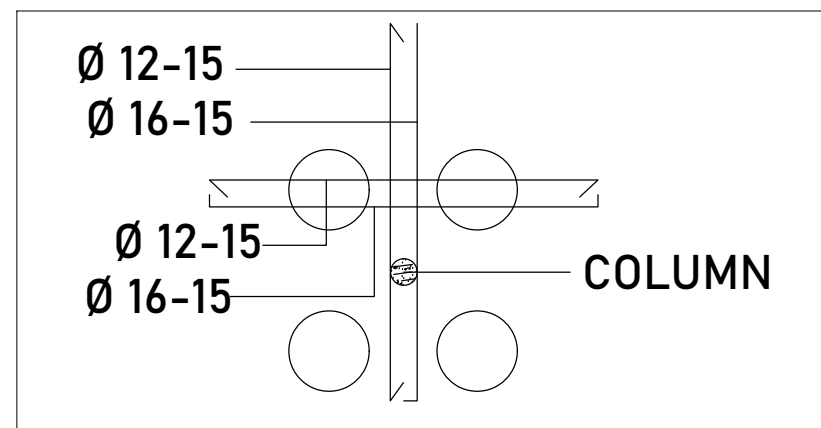

FOUNDATION PILE CAP DETAILS 2

Scale 1 : 20

NOTE

INSTITUTION



FACULTY OF ENGINEERING
UNIVERSITY SWADAYA GUNUNG
JATI CIREBON

TASK NAME

FINAL SEMESTER ASSIGNMENT

PROFESSION PLANNING
AND DESIGN
HIGH RISE BUILDING

MADE AS A FINAL SEMESTER
EXAMINATION ASSIGNMENT SCHOOL
YEAR 2020

LECTURER

Dr. SAIHUL ANWAR,Ir., M.Eng., MM.
NIDN. 417085401

INITIALS

DRAWN BY

MUHAMMAD NAZMI F
NPM. 120130085

INITIALS



IMAGE TITLE

HOTEL BUILDING
PLANNING WORK

IMAGE NAME

FOUNDATION PILE CAP
DETAILS 2

DATE	SCALE	DRAWING NUMBER	REVISION
03 FEBUARY 2021	1 : 20	11	-

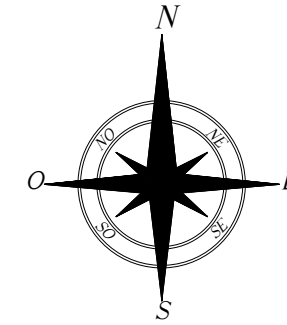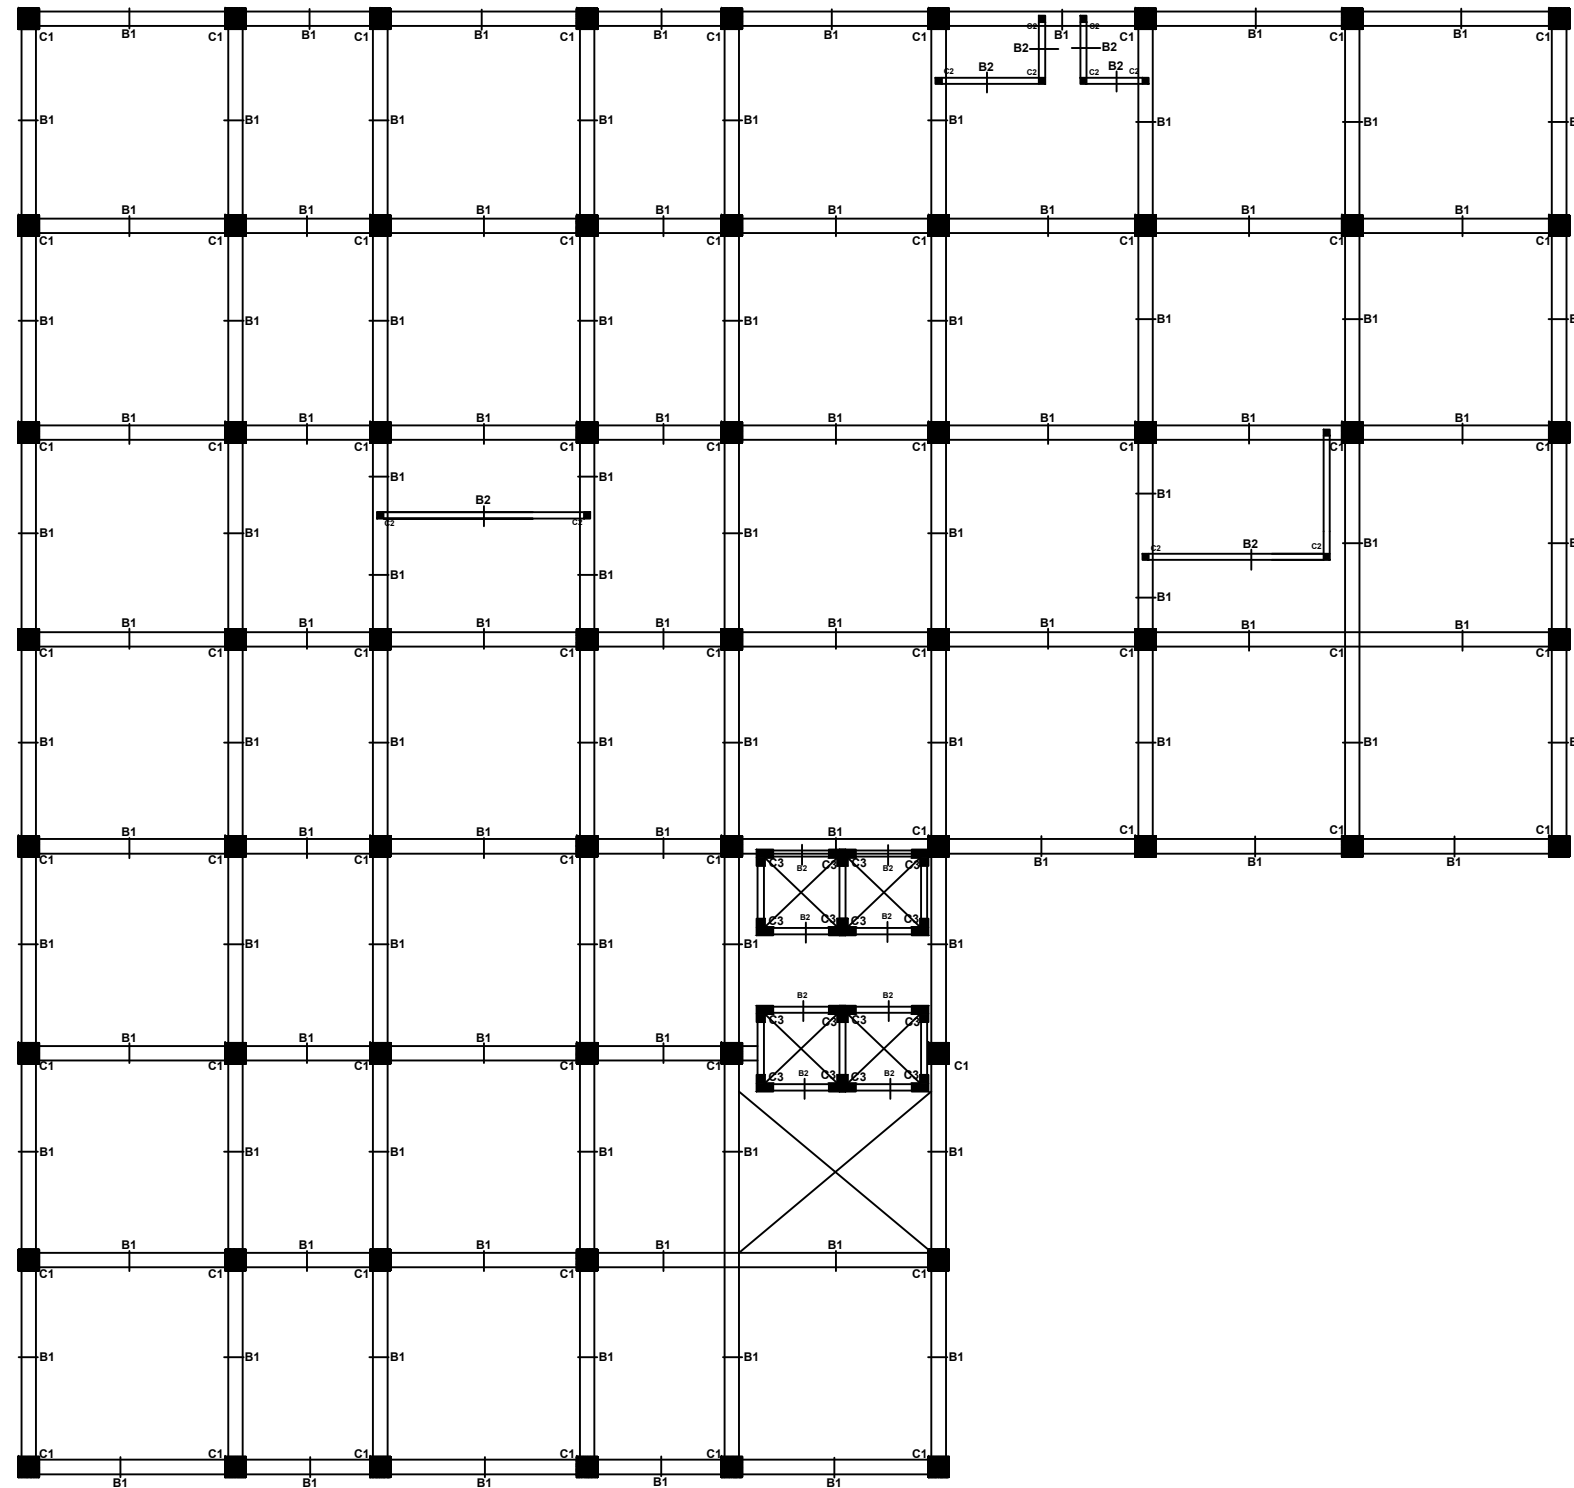

NOTE

B1 : 35CM X 60CM
B2 : 15CM X 30CM

C1 : 50CM X 50CM
C2 : 15CM X 15CM
C3 : 20CM X 40CM

INSTITUTION



FACULTY OF ENGINEERING
UNIVERSITY SWADAYA GUNUNG
JATI CIREBON

TASK NAME

FINAL SEMESTER ASSIGNMENT

PROFESSION PLANNING
AND DESIGN
HIGH RISE BUILDING

MADE AS A FINAL SEMESTER
EXAMINATION ASSIGNMENT SCHOOL
YEAR 2020

LECTURER

Dr. SAIHUL ANWAR,Ir., M.Eng., MM.
NIDN. 417085401

INITIALS

DRAWN BY

MUHAMMAD NAZMI F
NPM. 120130085

INITIALS

IMAGE TITLE

HOTEL BUILDING
PLANNING WORK



IMAGE NAME

FLOOR PLAN
COLUMN AND BEAM 1ST

DATE	SCALE	DRAWING NUMBER	REVISION
03 FEBUARY 2021	1 : 100	12	-

FLOOR PLAN COLUMN AND BEAM 1st

Skala 1 : 100

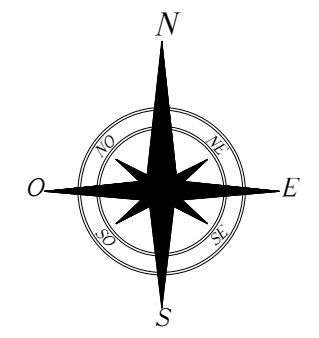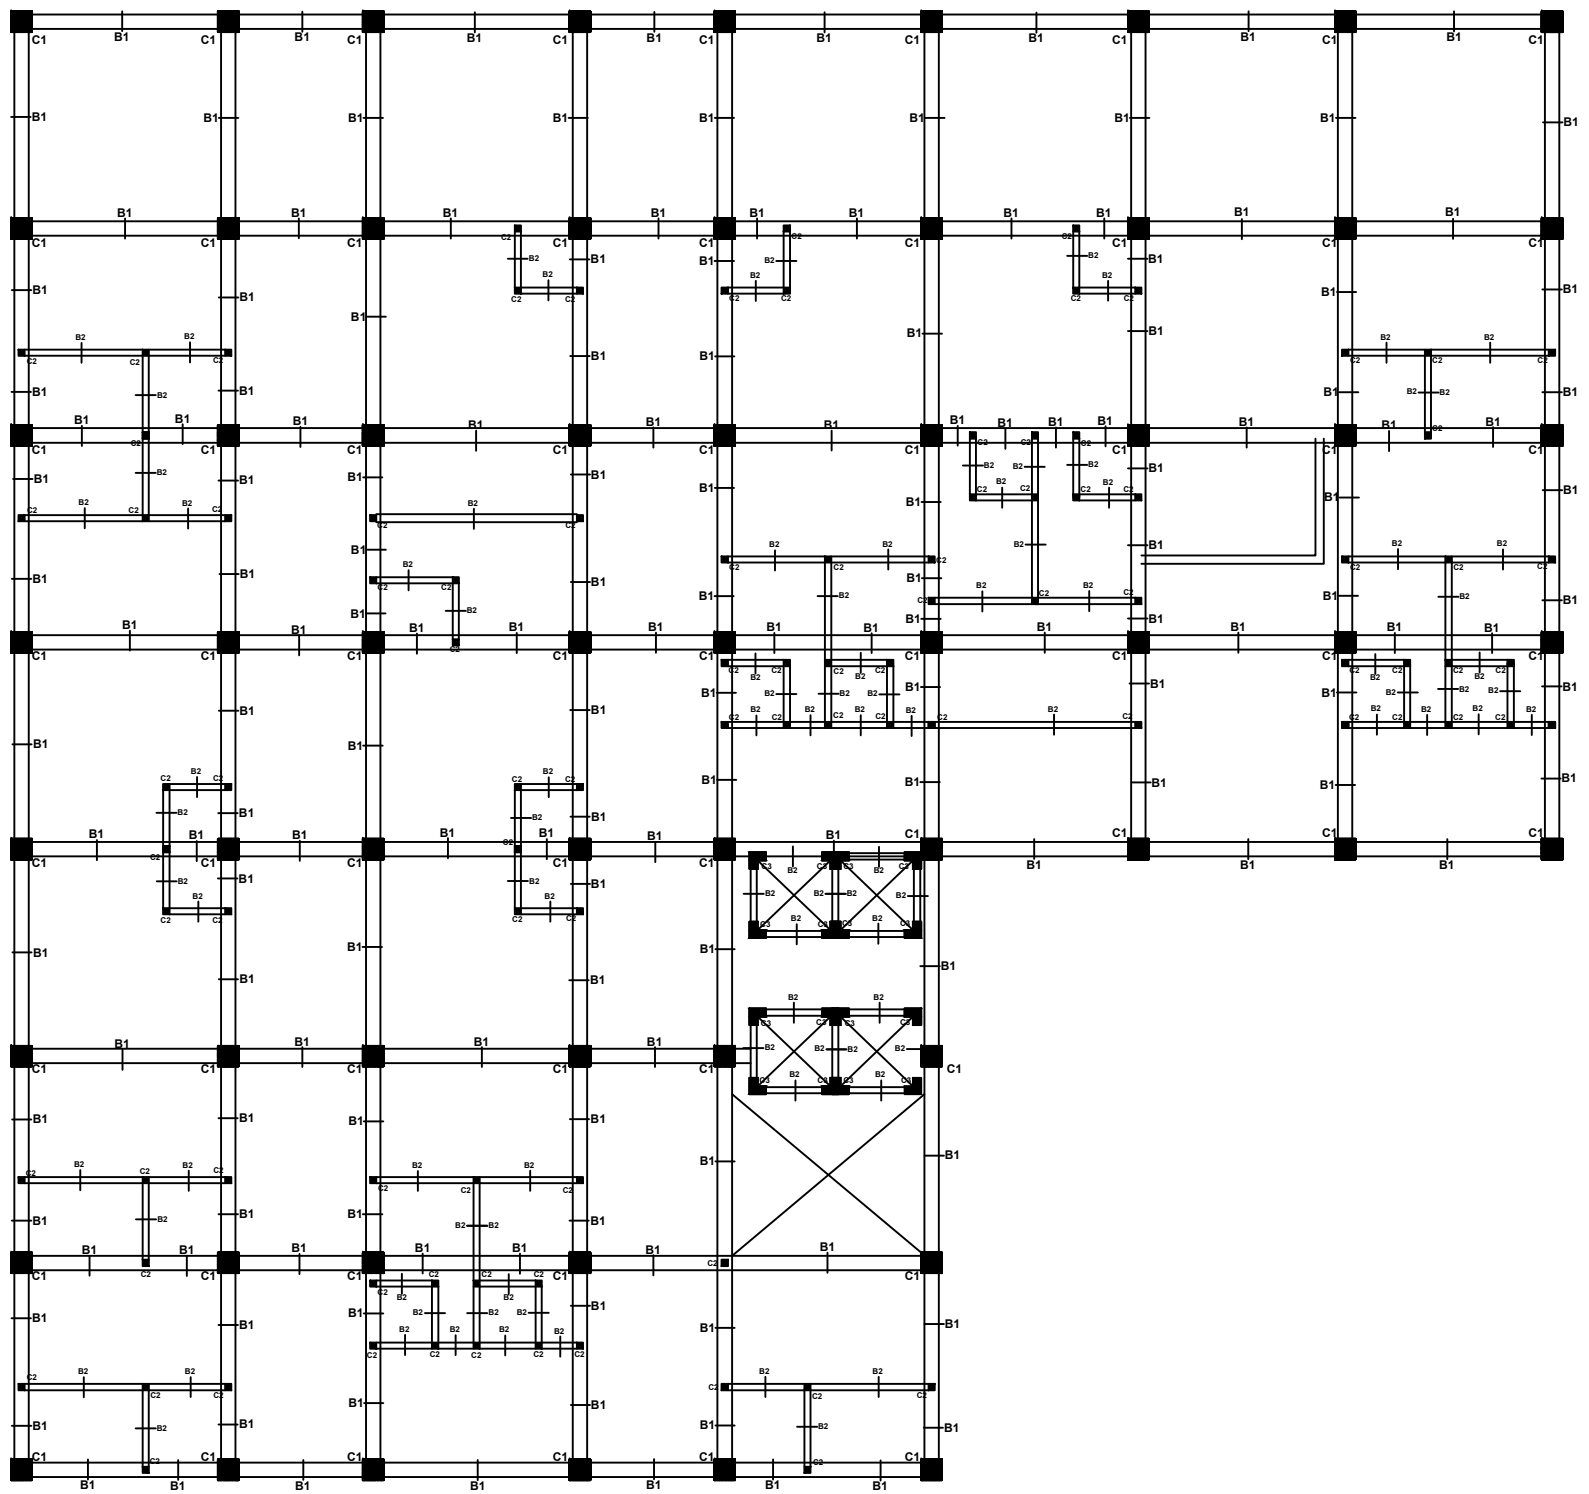

NOTE

B1 : 35CM X 60CM
B2 : 15CM X 30CM

C1 : 50CM X 50CM
C2 : 15CM X 15CM
C3 : 20CM X 40CM

INSTITUTION



FACULTY OF ENGINEERING
UNIVERSITY SWADAYA GUNUNG
JATI CIREBON

TASK NAME

FINAL SEMESTER ASSIGNMENT

PROFESSION PLANNING
AND DESIGN
HIGH RISE BUILDING

MADE AS A FINAL SEMESTER
EXAMINATION ASSIGNMENT SCHOOL
YEAR 2020

LECTURER

INITIALS

Dr. SAIHUL ANWAR,Ir., M.Eng., MM.
NIDN. 417085401

DRAWN BY

INITIALS

MUHAMMAD NAZMI F
NPM. 120130085

IMAGE TITLE

HOTEL BUILDING
PLANNING WORK



IMAGE NAME

FLOOR PLAN
COLUMN AND BEAM 2nd

DATE	SCALE	DRAWING NUMBER	REVISION
03 FEBUARY 2021	1 : 100	13	-

FLOOR PLAN COLUMN AND BEAM 2nd

Skala 1 : 100

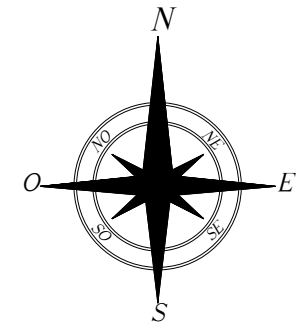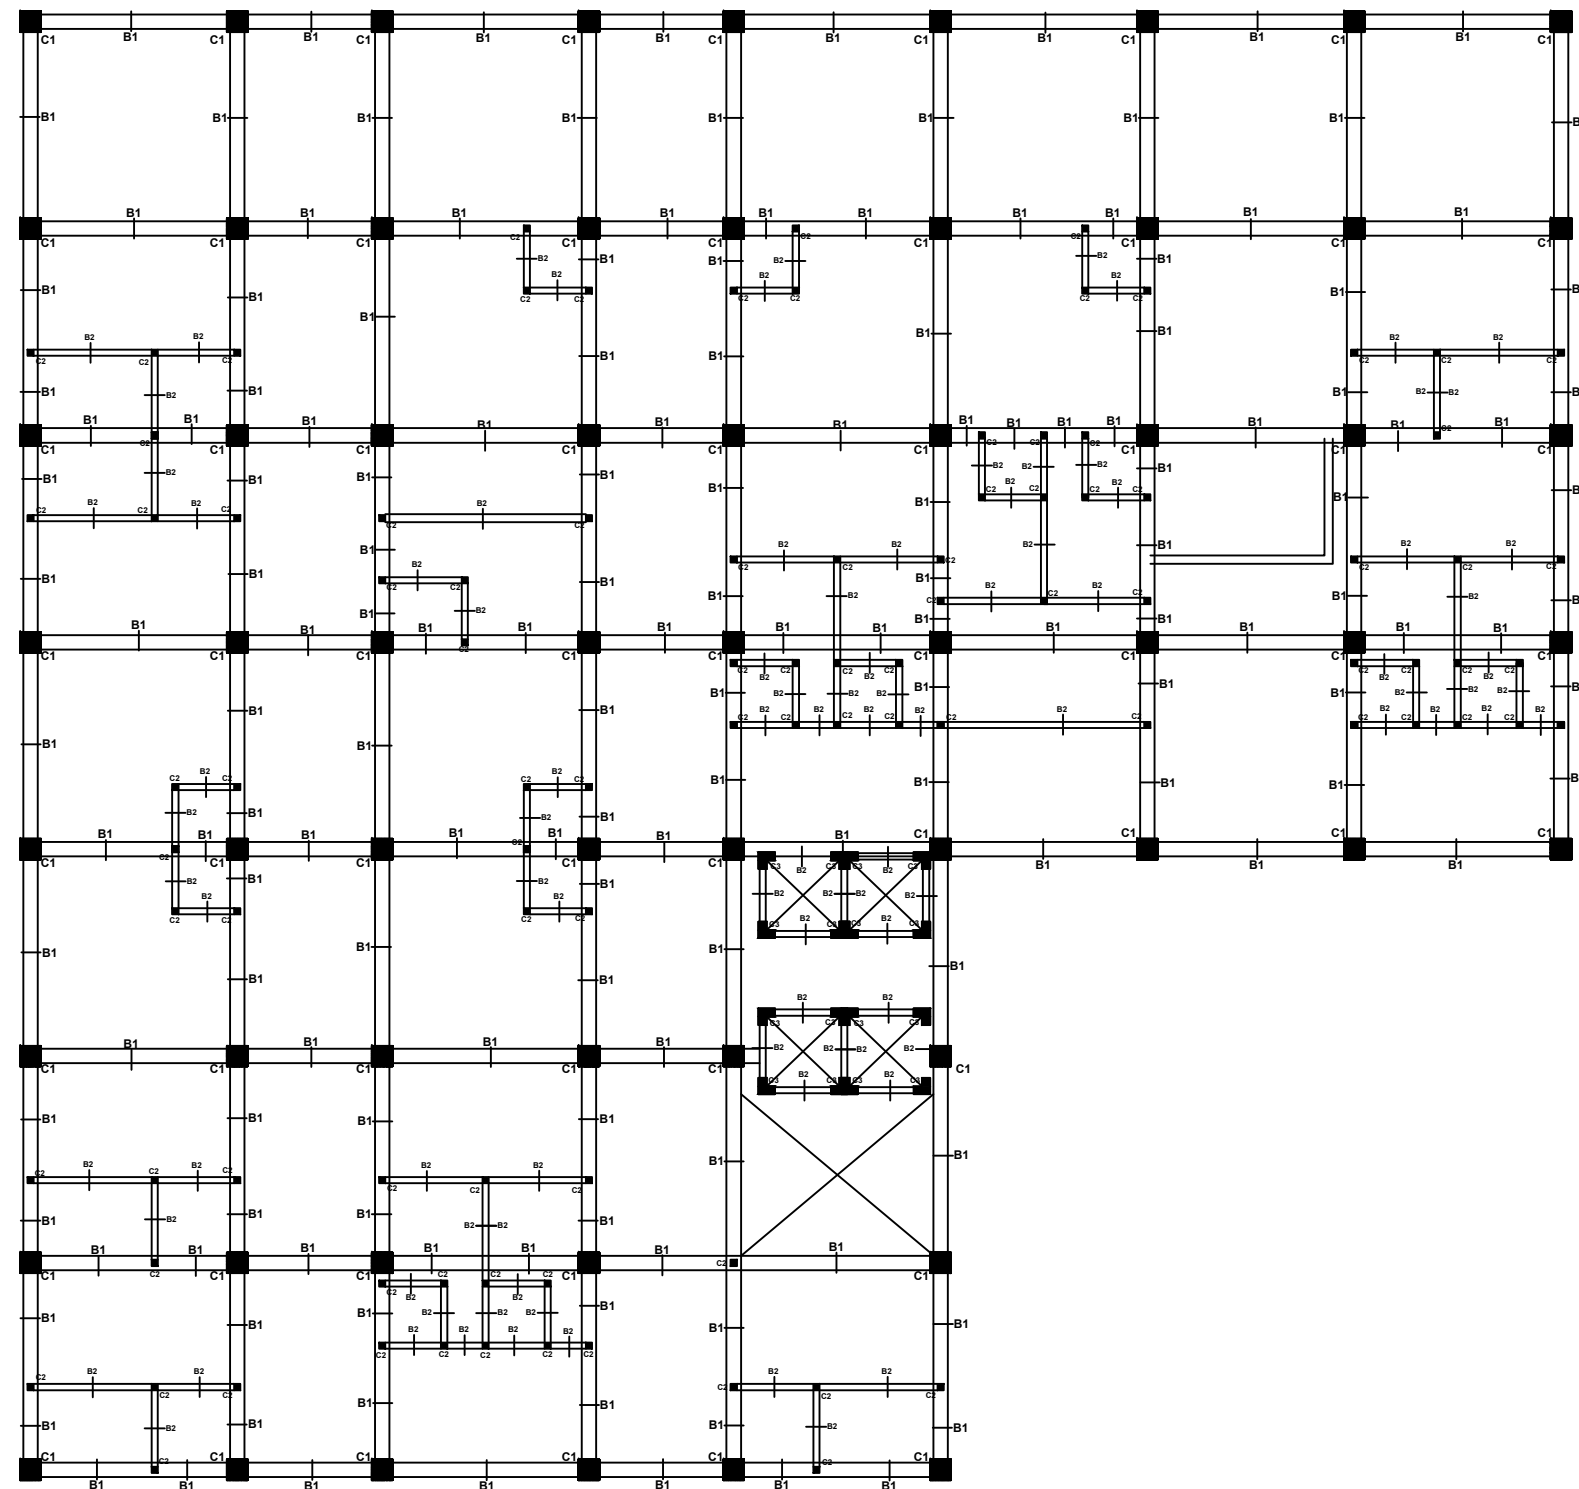

NOTE

B1 : 35CM X 60CM
B2 : 15CM X 30CM

C1 : 50CM X 50CM
C2 : 15CM X 15CM
C3 : 20CM X 40CM

INSTITUTION



FACULTY OF ENGINEERING
UNIVERSITY SWADAYA GUNUNG
JATI CIREBON

TASK NAME

FINAL SEMESTER ASSIGNMENT

PROFESSION PLANNING
AND DESIGN
HIGH RISE BUILDING

MADE AS A FINAL SEMESTER
EXAMINATION ASSIGNMENT SCHOOL
YEAR 2020

LECTURER

INITIALS

Dr. SAIHUL ANWAR,Ir., M.Eng., MM.
NIDN. 417085401

DRAWN BY

INITIALS

MUHAMMAD NAZMI F
NPM. 120130085

IMAGE TITLE

HOTEL BUILDING
PLANNING WORK



IMAGE NAME

FLOOR PLAN
COLUMN AND BEAM 3rd

DATE	SCALE	DRAWING NUMBER	REVISION
03 FEBUARY 2021	1 : 100	14	-

FLOOR PLAN COLUMN AND BEAM 3rd

Skala 1 : 100

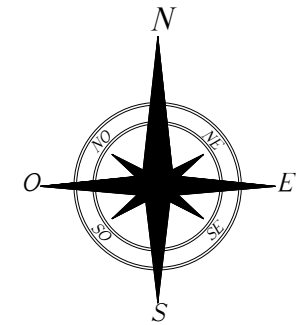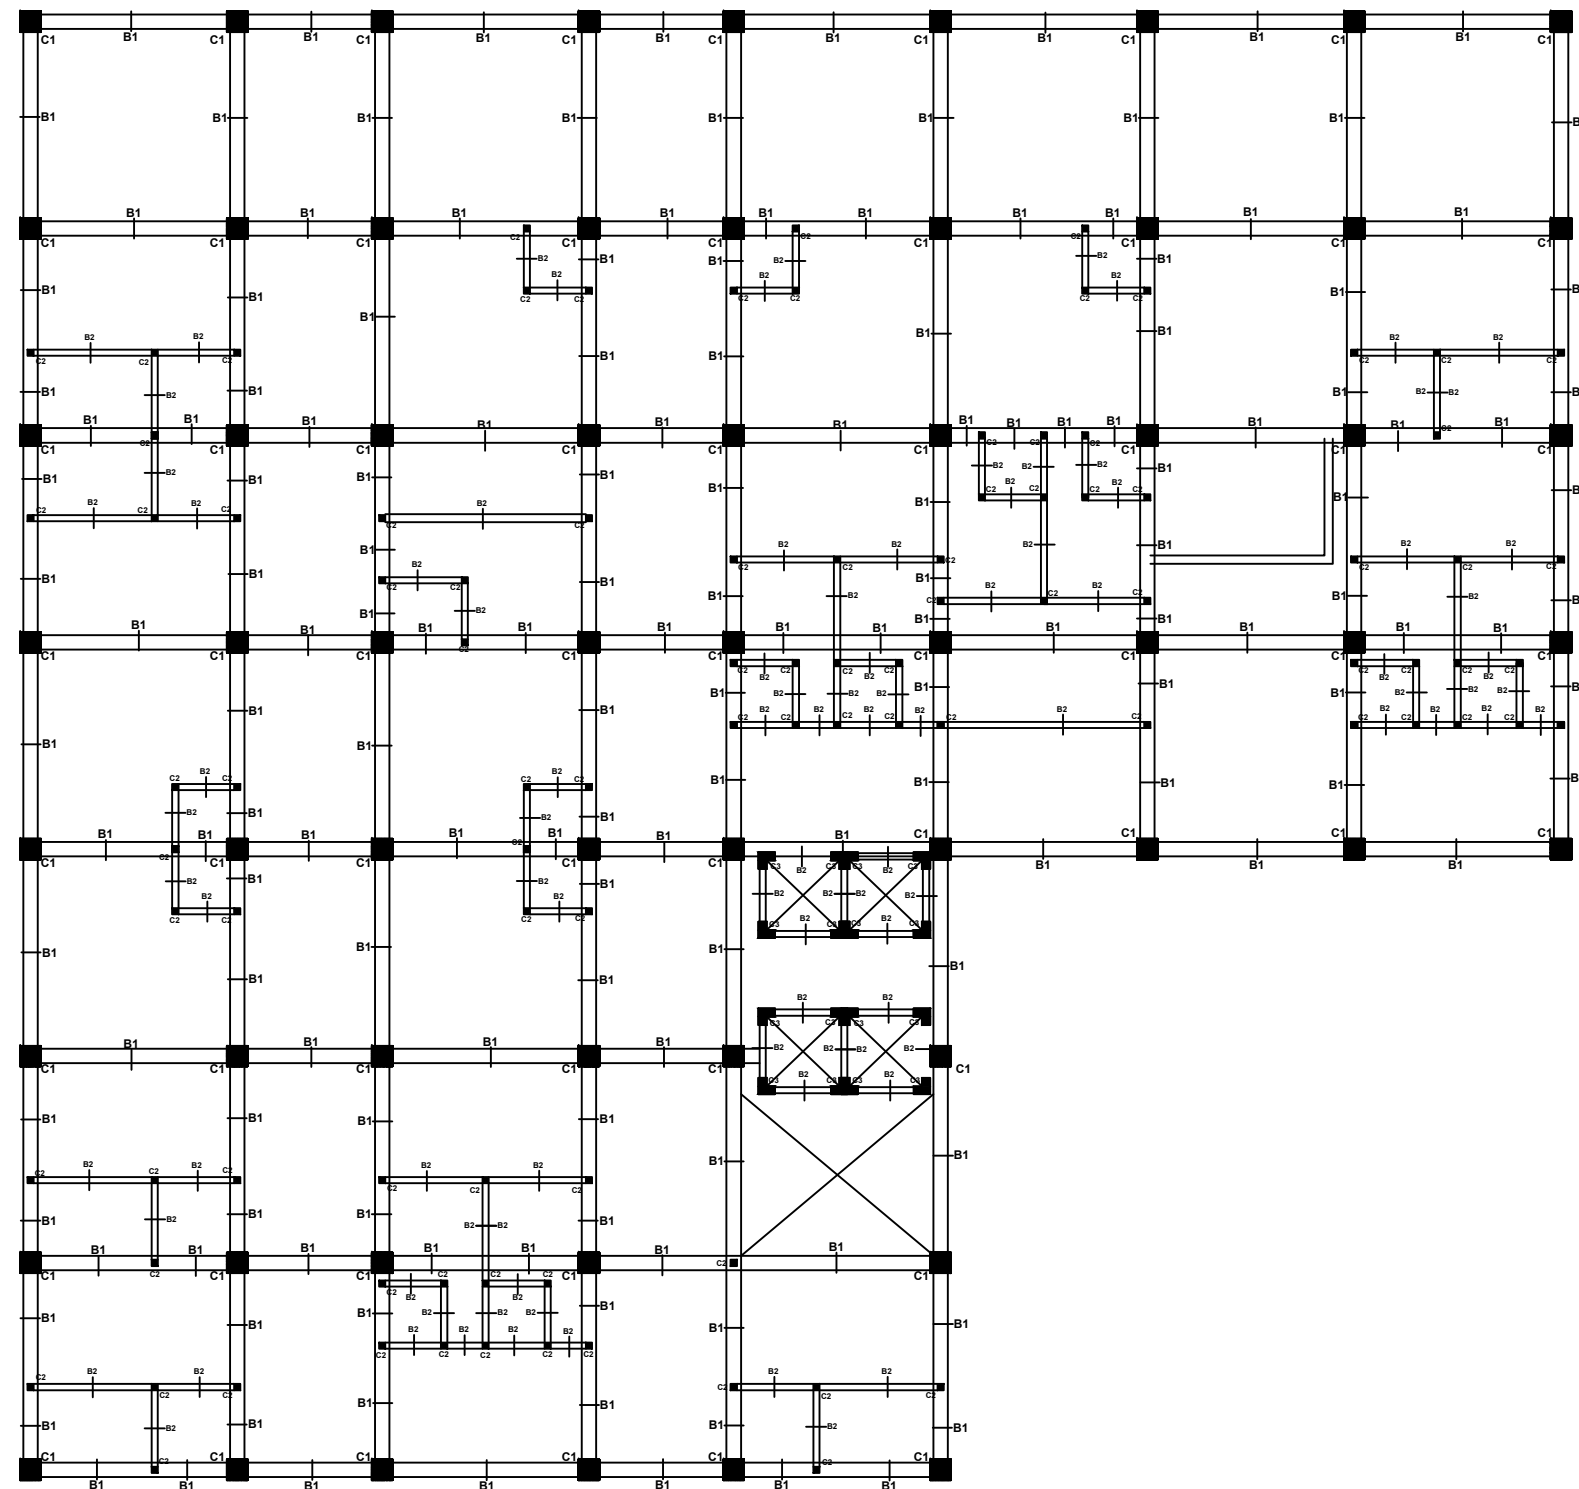

NOTE

B1 : 35CM X 60CM
B2 : 15CM X 30CM

C1 : 50CM X 50CM
C2 : 15CM X 15CM
C3 : 20CM X 40CM

INSTITUTION



FACULTY OF ENGINEERING
UNIVERSITY SWADAYA GUNUNG
JATI CIREBON

TASK NAME

FINAL SEMESTER ASSIGNMENT

PROFESSION PLANNING
AND DESIGN
HIGH RISE BUILDING

MADE AS A FINAL SEMESTER
EXAMINATION ASSIGNMENT SCHOOL
YEAR 2020

LECTURER

INITIALS

Dr. SAIHUL ANWAR,Ir., M.Eng., MM.
NIDN. 417085401

DRAWN BY

INITIALS

MUHAMMAD NAZMI F
NPM. 120130085

IMAGE TITLE

HOTEL BUILDING
PLANNING WORK

IMAGE NAME

FLOOR PLAN
COLUMN AND BEAM 4th

DATE	SCALE	DRAWING NUMBER	REVISION
03 FEBUARY 2021	1 : 100	15	-

FLOOR PLAN COLUMN AND BEAM 4th

Skala 1 : 100

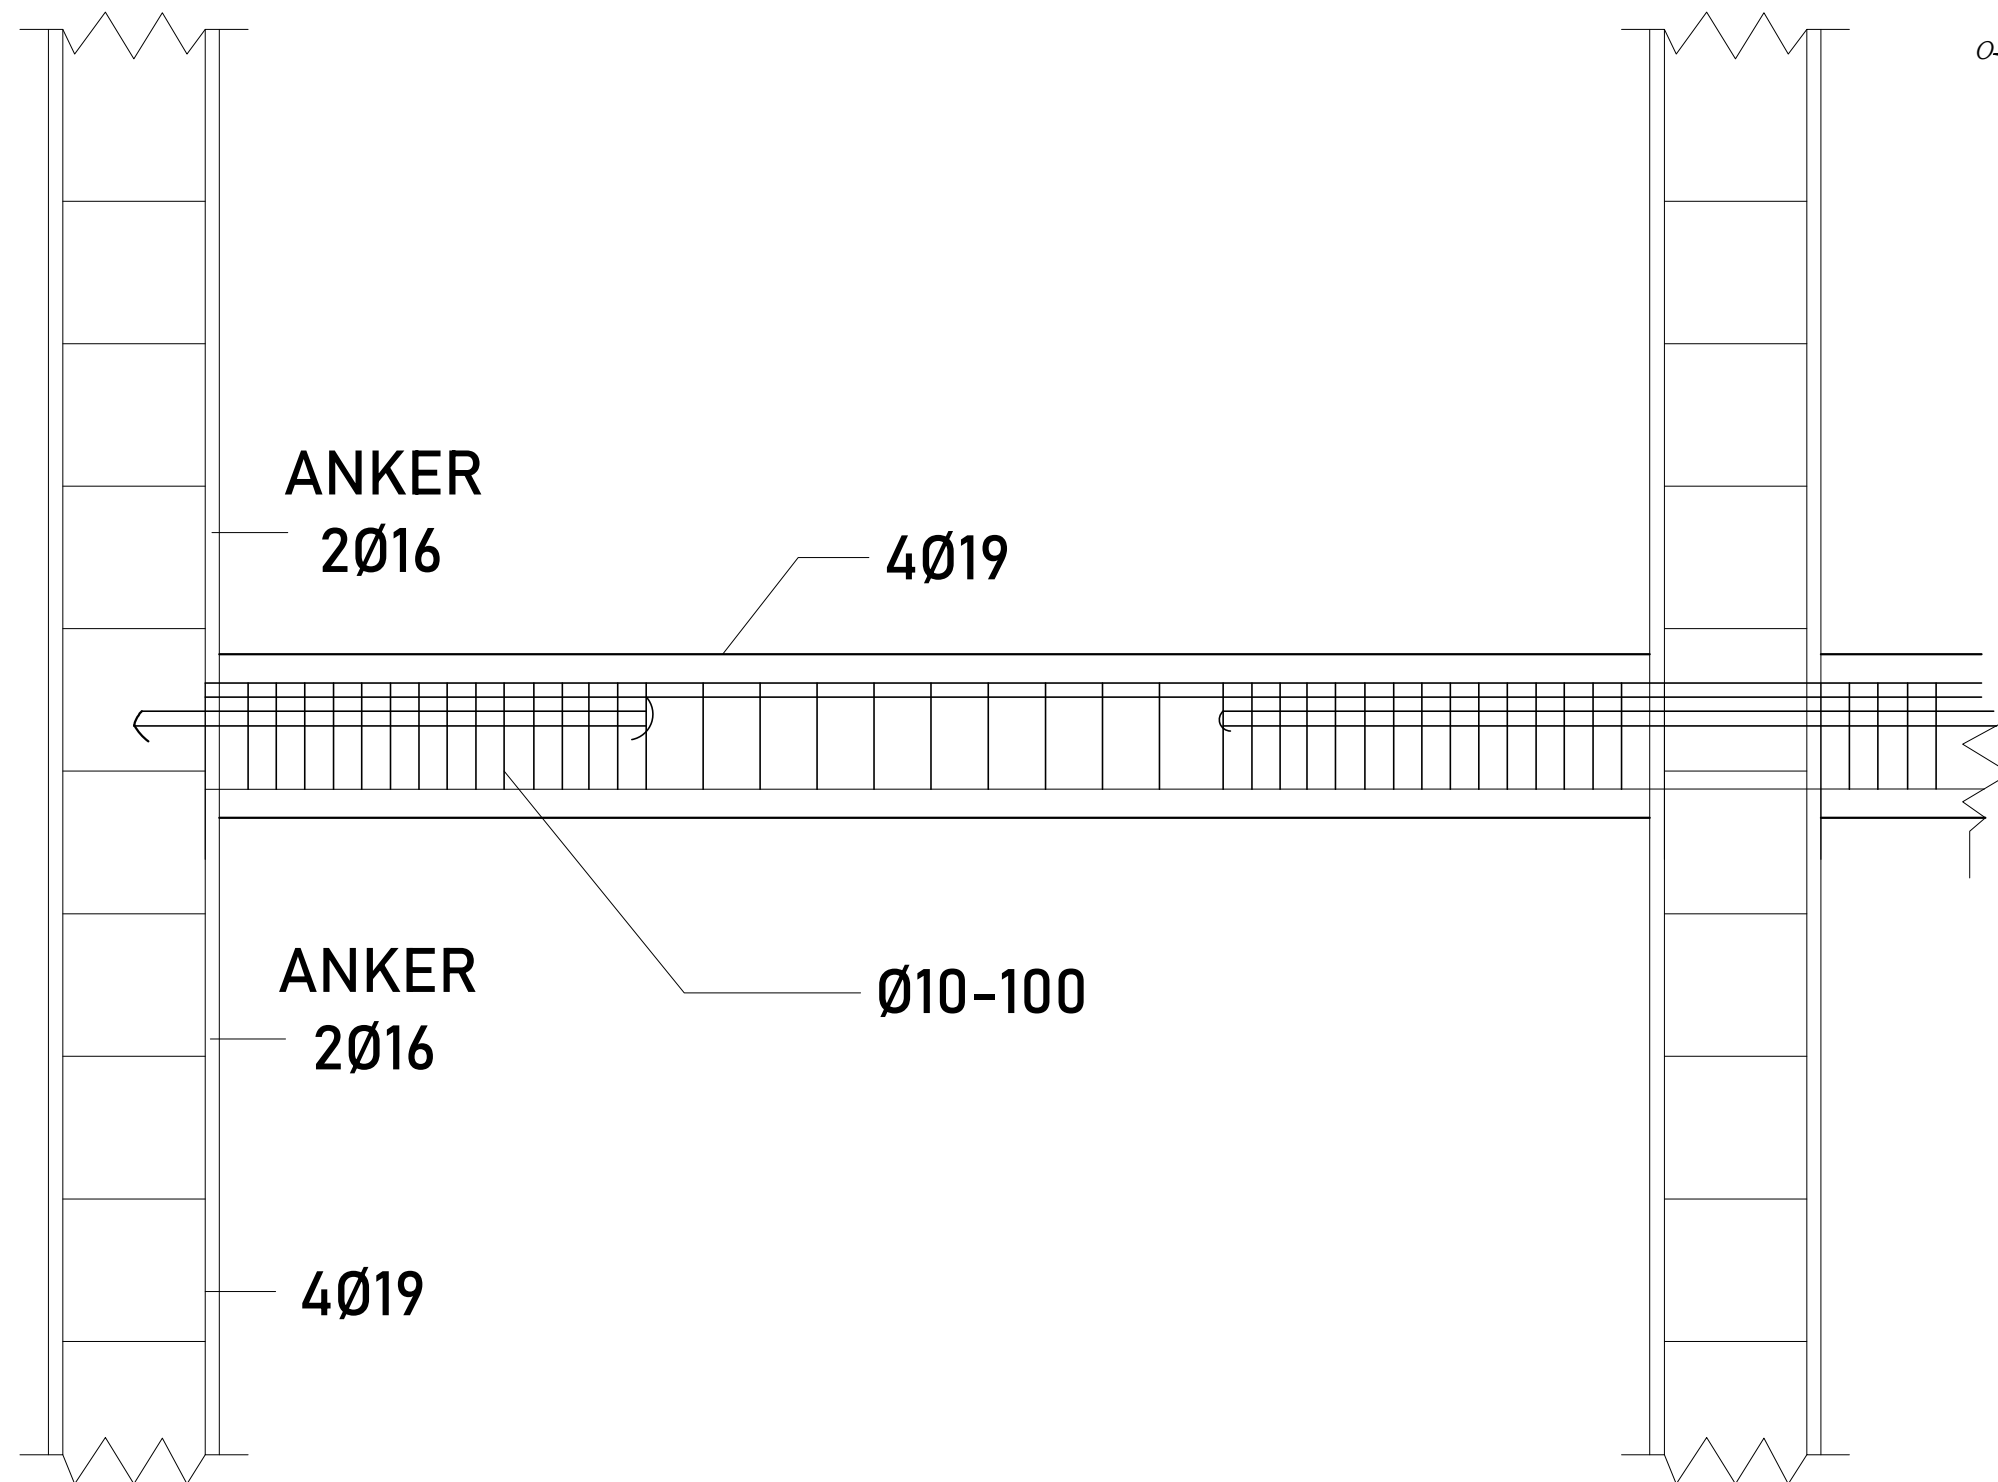


PLATE REINFORCEMENT DETAIL

Scale 1 : 20

NOTE

INSTITUTION



FACULTY OF ENGINEERING
UNIVERSITY SWADAYA GUNUNG
JATI CIREBON

TASK NAME

FINAL SEMESTER ASSIGNMENT

PROFESSION PLANNING
AND DESIGN
HIGH RISE BUILDING

MADE AS A FINAL SEMESTER
EXAMINATION ASSIGNMENT SCHOOL
YEAR 2020

LECTURER

INITIALS

Dr. SAIHUL ANWAR,Ir., M.Eng., MM.
NIDN. 417085401

DRAWN BY

INITIALS

MUHAMMAD NAZMI F
NPM. 120130085





IMAGE TITLE

HOTEL BUILDING
PLANNING WORK

IMAGE NAME

PLATE REINFORCEMENT
DETAIL



DATE	SCALE	DRAWING NUMBER	REVISION
03 FEBUARY 2021	1 : 20	16	-

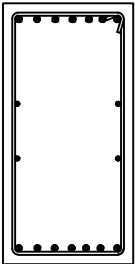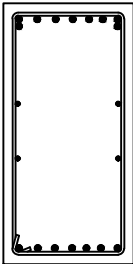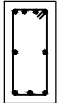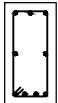NAME	BEAM 1 (B1)	BEAM 2 (B2)	BEAM 1 (B1)	BEAM 2 (B2)
LOCATION	PEDESTAL	FIELD	PEDESTAL	FIELD
DETAIL				
SIZE	35 x 60	35 x 60	15 x 30	15 x 30
REINFORCING BAR	4 Ø12	5 Ø12	4 Ø12	3 Ø12
BOTTOM REINFORCE	5 Ø12	4 Ø12	3 Ø12	4 Ø12
SIDE REINFORCE	3 Ø12	3 Ø12	1 Ø12	1 Ø12
PEDESTAL	Ø10-20	Ø10-20	Ø10-20	Ø10-20

DETAILS BEAM

SCALE 1:20

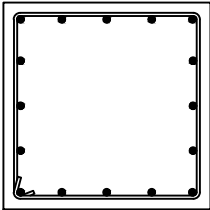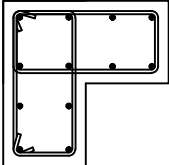

NAME	COLUMN 1 (C1)	COLUMN 2 (C2)	COLUMN 3 (C3)
LOCATION	ALL	ALL	ALL
DETAIL			
SIZE	50 x 50	15 x 15	20 x 40
REINFORCING BAR	3 Ø12	2 Ø12	2 Ø12
BOTTOM REINFORCE	3 Ø12	2 Ø12	2 Ø12
SIDE REINFORCE	1 Ø12	—	—
PEDESTAL	Ø10-20	Ø10-20	Ø10-20

DETAILS COLUMN

SCALE 1:20



NOTE

INSTITUTION



FACULTY OF ENGINEERING
UNIVERSITY SWADAYA GUNUNG
JATI CIREBON

TASK NAME

FINAL SEMESTER ASSIGNMENT

PROFESSION PLANNING
AND DESIGN
HIGH RISE BUILDING

MADE AS A FINAL SEMESTER
EXAMINATION ASSIGNMENT SCHOOL
YEAR 2020

LECTURER

INITIALS

Dr. SAIHUL ANWAR,Ir., M.Eng., MM.
NIDN. 417085401

DRAWN BY

INITIALS

MUHAMMAD NAZMI F
NMP. 120130085

IMAGE TITLE

HOTEL BUILDING
PLANNING WORK


IMAGE NAME



DETAILS BEAM AND COLUMN

DATE	SCALE	DRAWING NUMBER	REVISION
03 FEBUARY 2021	1 : 100	17	-

DETAILS BEAM AND COLUMN

Scale 1 : 20

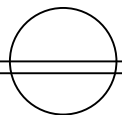

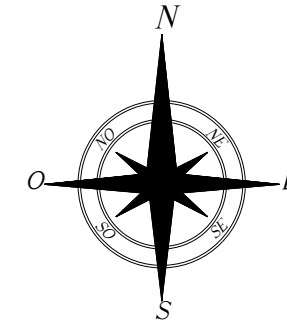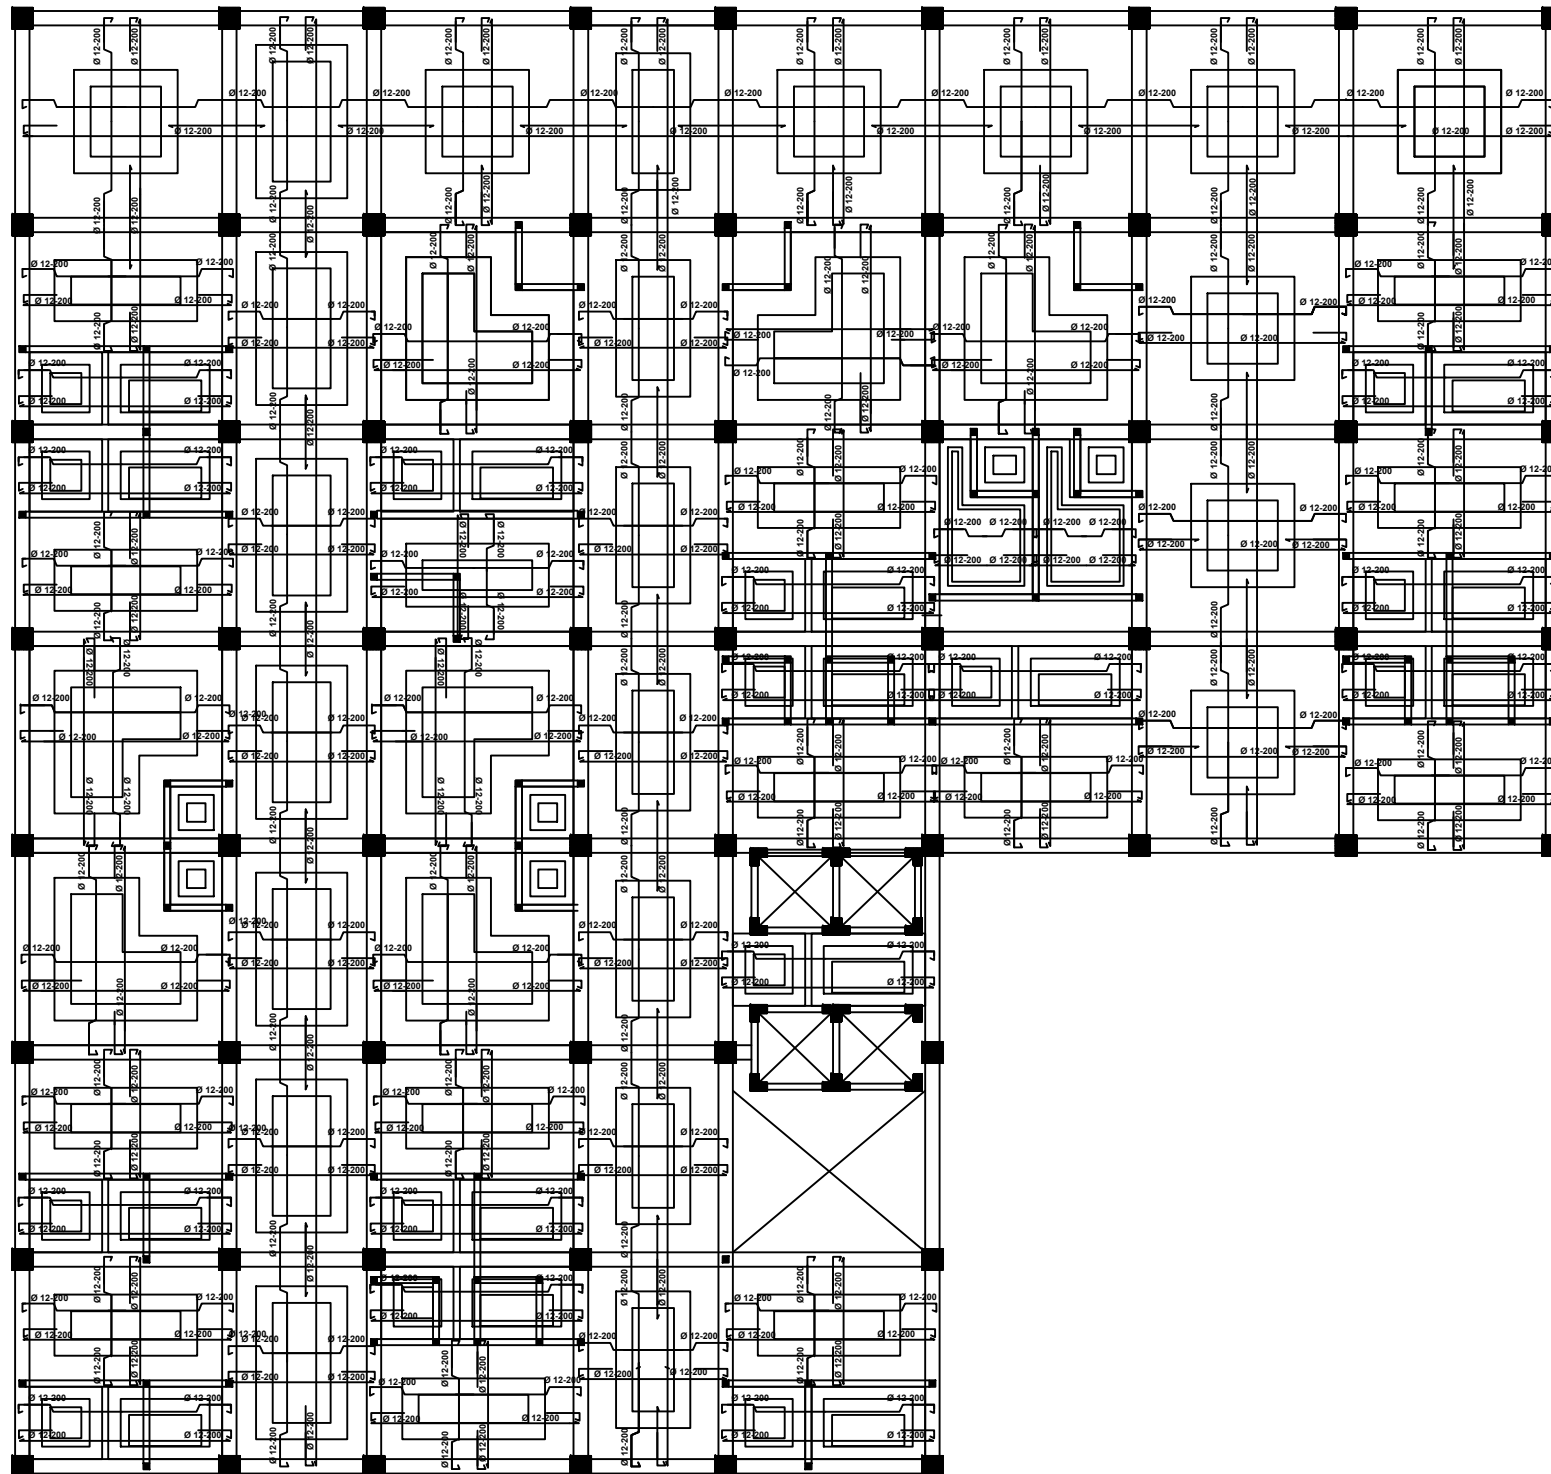

FLATE REINFORCEMENT PLAN 2nd

Skala 1 : 100

NOTE

INSTITUTION



FACULTY OF ENGINEERING
UNIVERSITY SWADAYA GUNUNG
JATI CIREBON

TASK NAME

FINAL SEMESTER ASSIGNMENT

PROFESSION PLANNING
AND DESIGN
HIGH RISE BUILDING

MADE AS A FINAL SEMESTER
EXAMINATION ASSIGMENT SCHOOL
YEAR 2020

LECTURER

INITIALS

Dr. SAIHUL ANWAR,Ir., M.Eng., MM.
NIDN. 417085401

DRAWN BY

INITIALS

MUHAMMAD NAZMI F
NPM. 120130085



IMAGE TITLE

HOTEL BUILDING
PLANNING WORK

IMAGE NAME

FLATE REINFORCEMENT
PLAN 2nd

DATE	SCALE	DRAWING NUMBER	REVISION
03 FEBUARY 2021	1 : 100	18	-

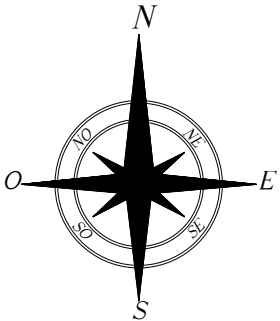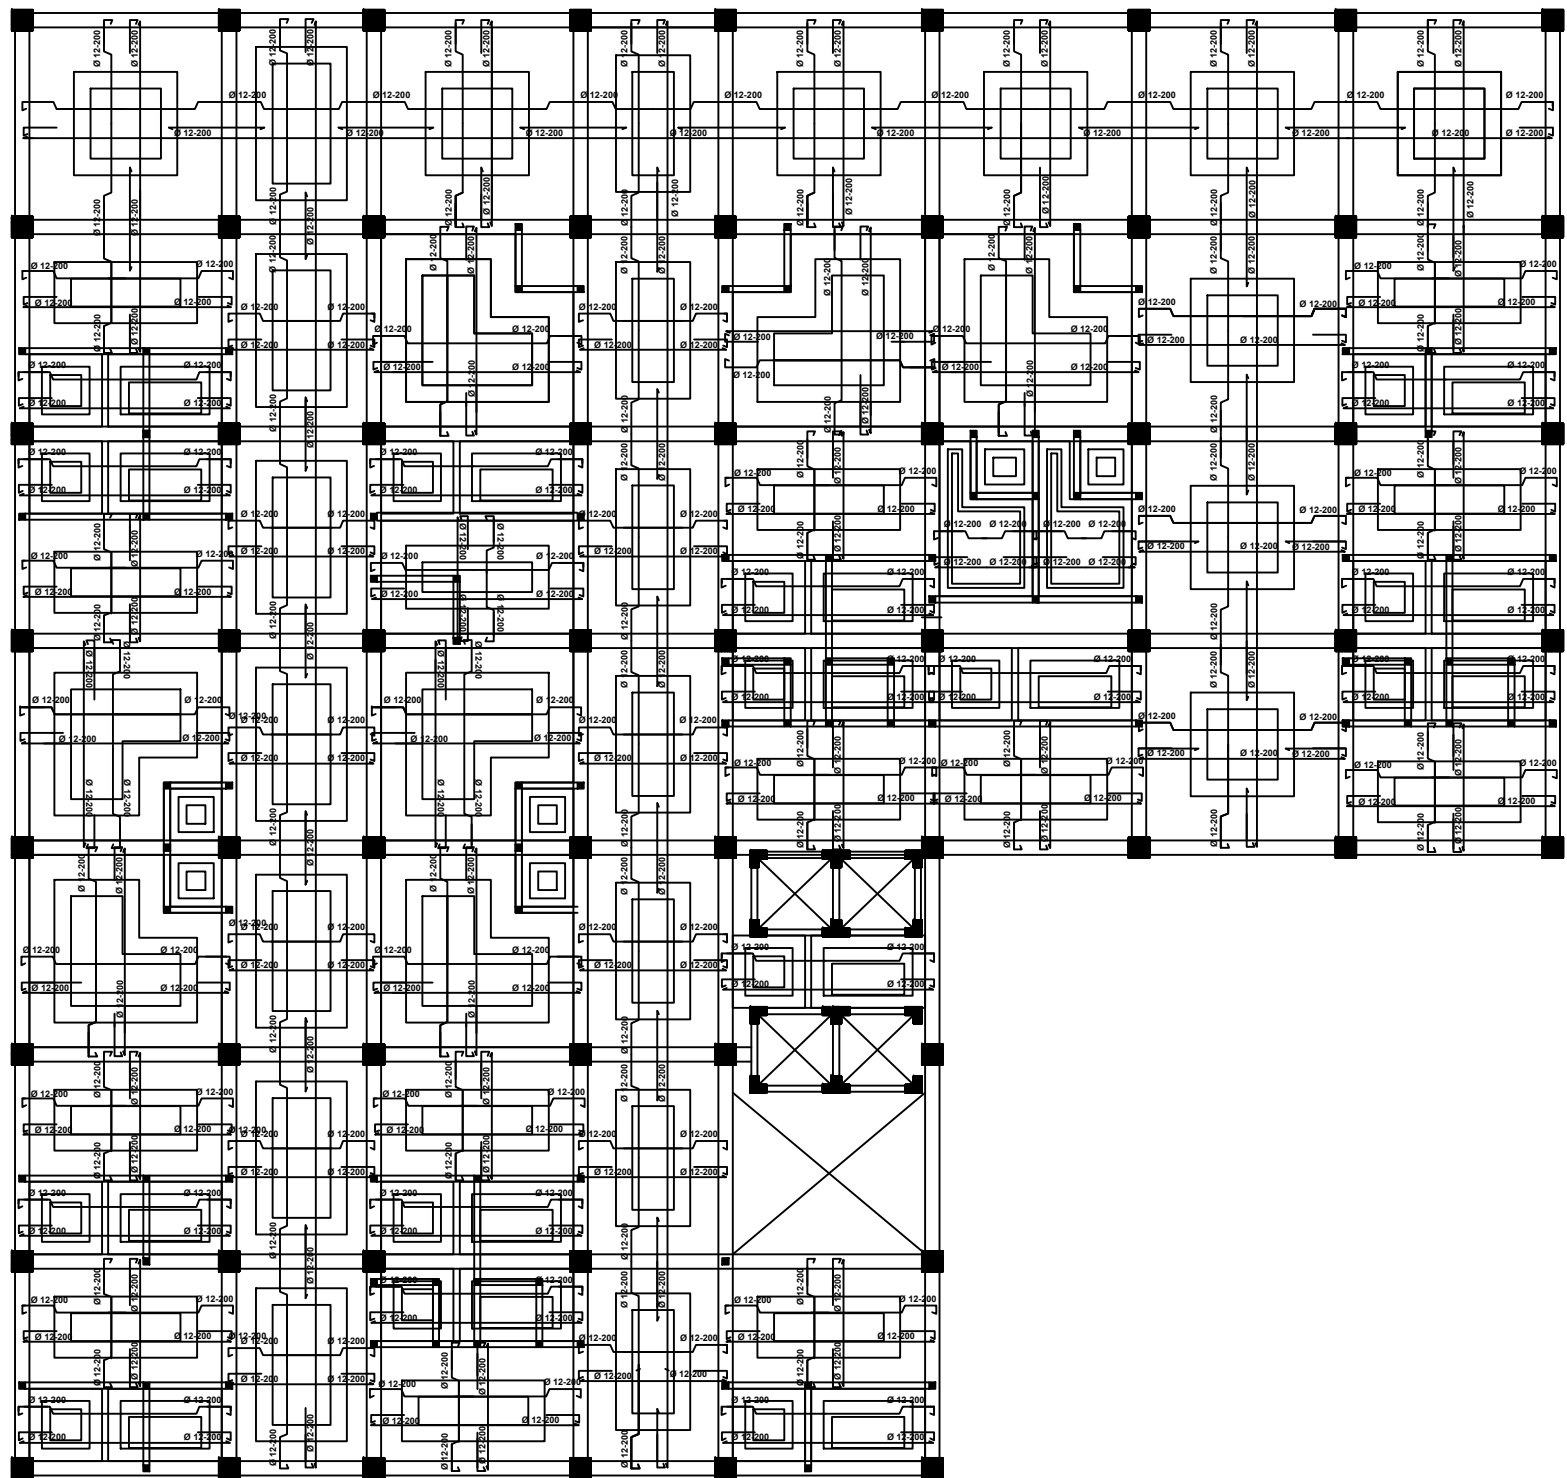

FLATE REINFORCEMENT PLAN 3rd

Skala 1 : 100

NOTE

INSTITUTION



FACULTY OF ENGINEERING
UNIVERSITY SWADAYA GUNUNG
JATI CIREBON

TASK NAME

FINAL SEMESTER ASSIGNMENT

PROFESSION PLANNING
AND DESIGN
HIGH RISE BUILDING

MADE AS A FINAL SEMESTER
EXAMINATION ASSIGMENT SCHOOL
YEAR 2020

LECTURER

INITIALS

Dr. SAIHUL ANWAR,Ir., M.Eng., MM.
NIDN. 417085401

DRAWN BY

INITIALS

MUHAMMAD NAZMI F
NPM. 120130085



IMAGE TITLE

HOTEL BUILDING
PLANNING WORK

IMAGE NAME

FLATE REINFORCEMENT
PLAN 3rd

DATE	SCALE	DRAWING NUMBER	REVISION
03 FEBUARY 2021	1 : 100	19	-

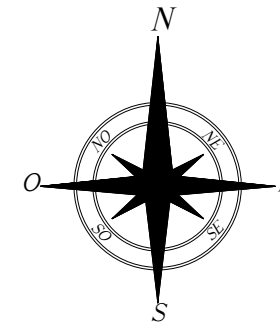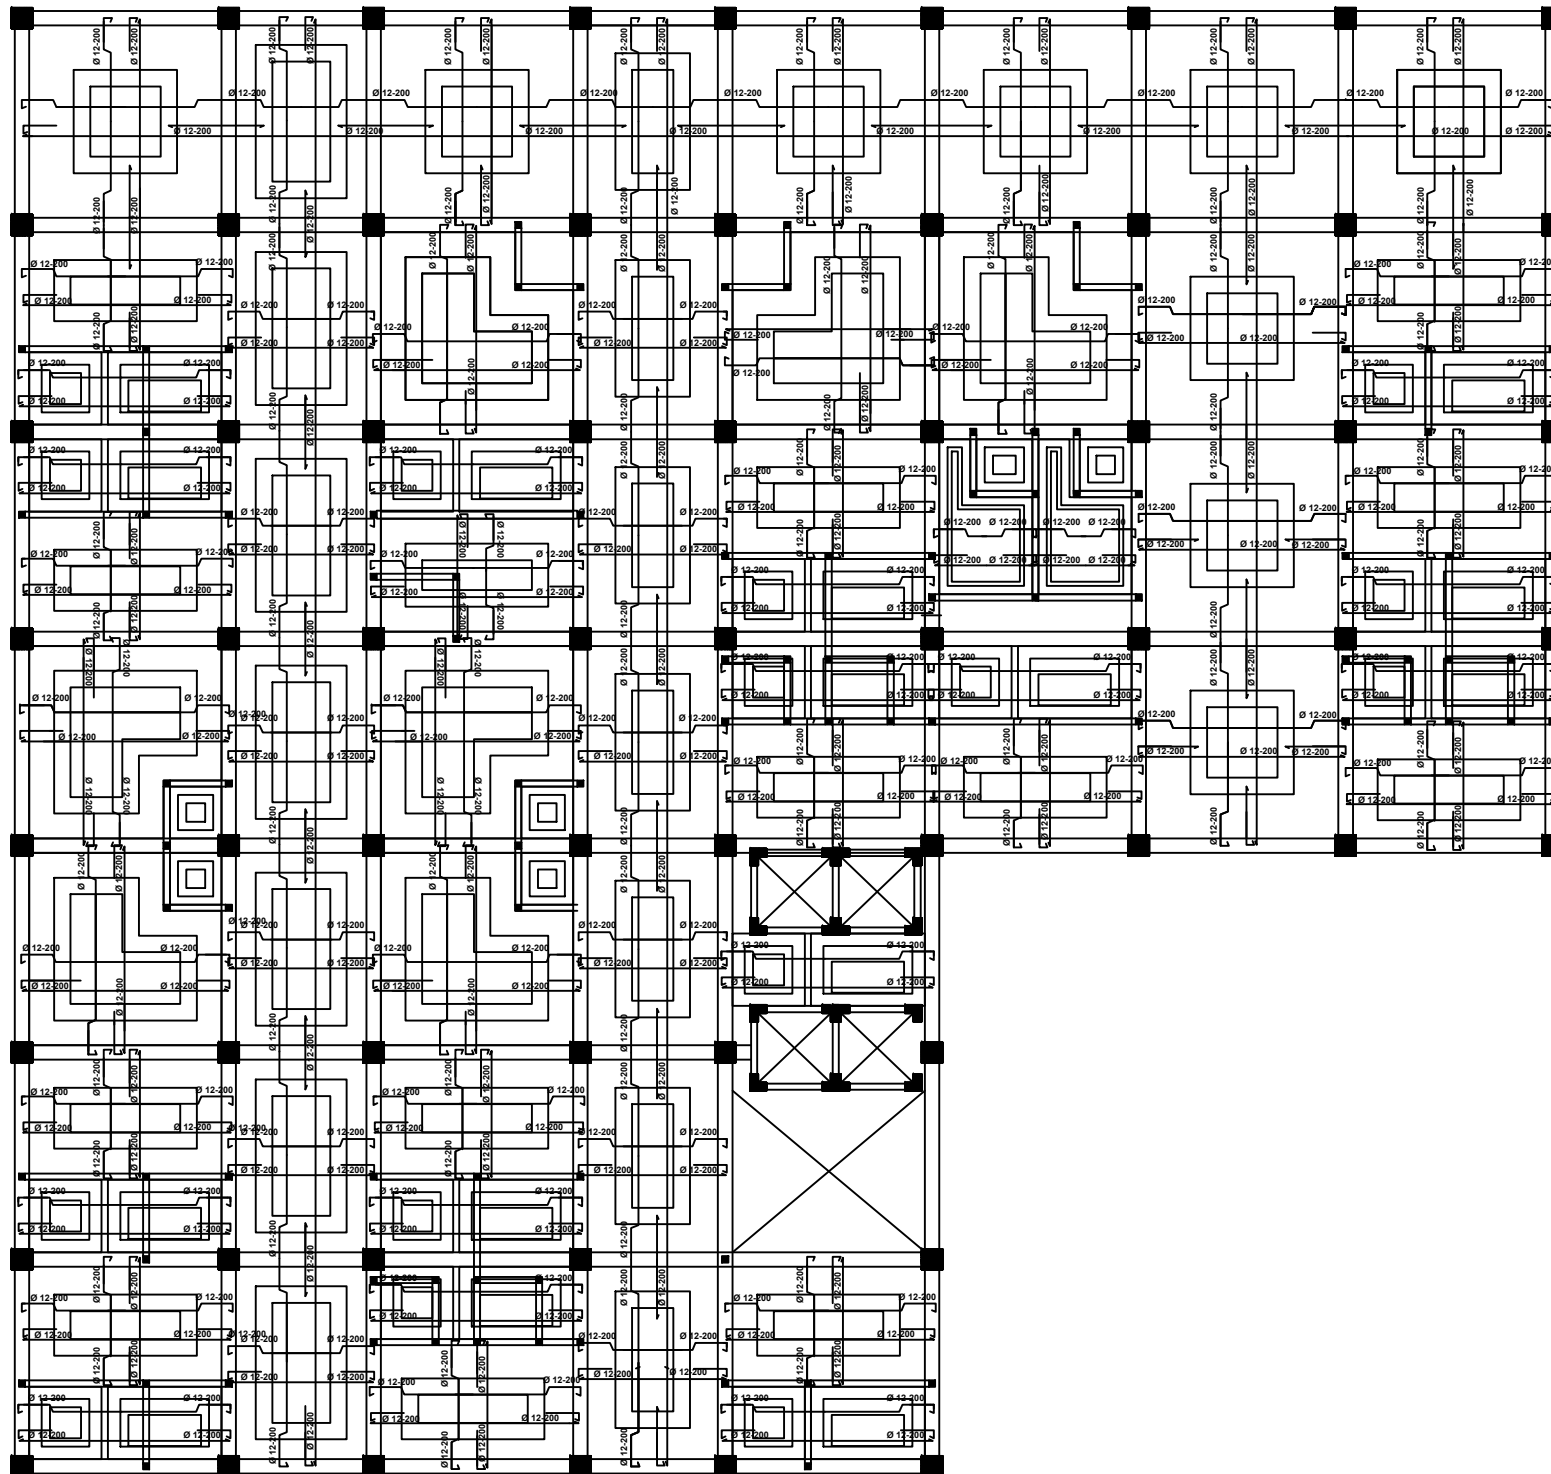

FLATE REINFORCEMENT PLAN 4th

Skala 1 : 100

NOTE

INSTITUTION



FACULTY OF ENGINEERING
UNIVERSITY SWADAYA GUNUNG
JATI CIREBON

TASK NAME

FINAL SEMESTER ASSIGNMENT

PROFESSION PLANNING
AND DESIGN
HIGH RISE BUILDING

MADE AS A FINAL SEMESTER
EXAMINATION ASSIGMENT SCHOOL
YEAR 2020

LECTURER

Dr. SAIHUL ANWAR,Ir., M.Eng., MM.
NIDN. 417085401

DRAWN BY

MUHAMMAD NAZMI F
NPM. 120130085




IMAGE TITLE

HOTEL BUILDING
PLANNING WORK

IMAGE NAME

FLATE REINFORCEMENT
PLAN 4th

DATE	SCALE	DRAWING NUMBER	REVISION
03 FEBUARY 2021	1 : 100	20	-

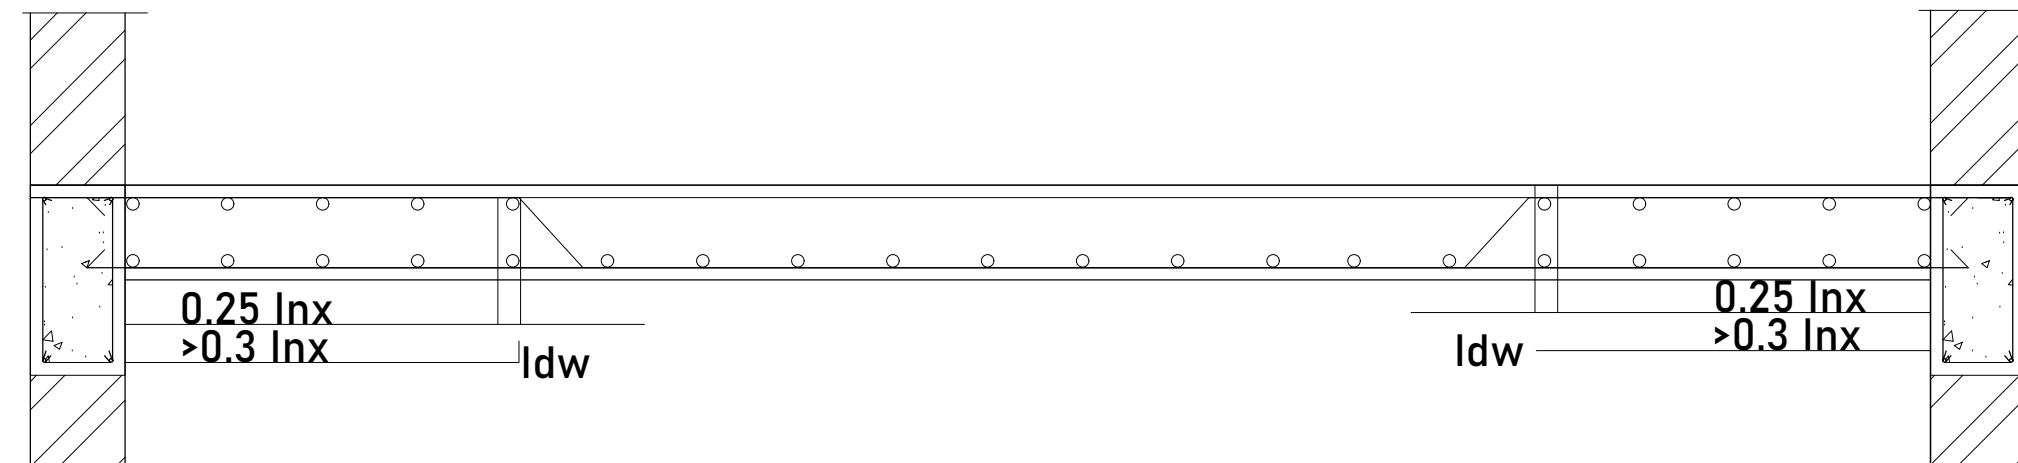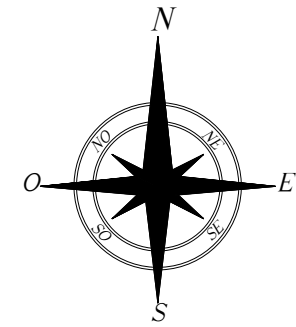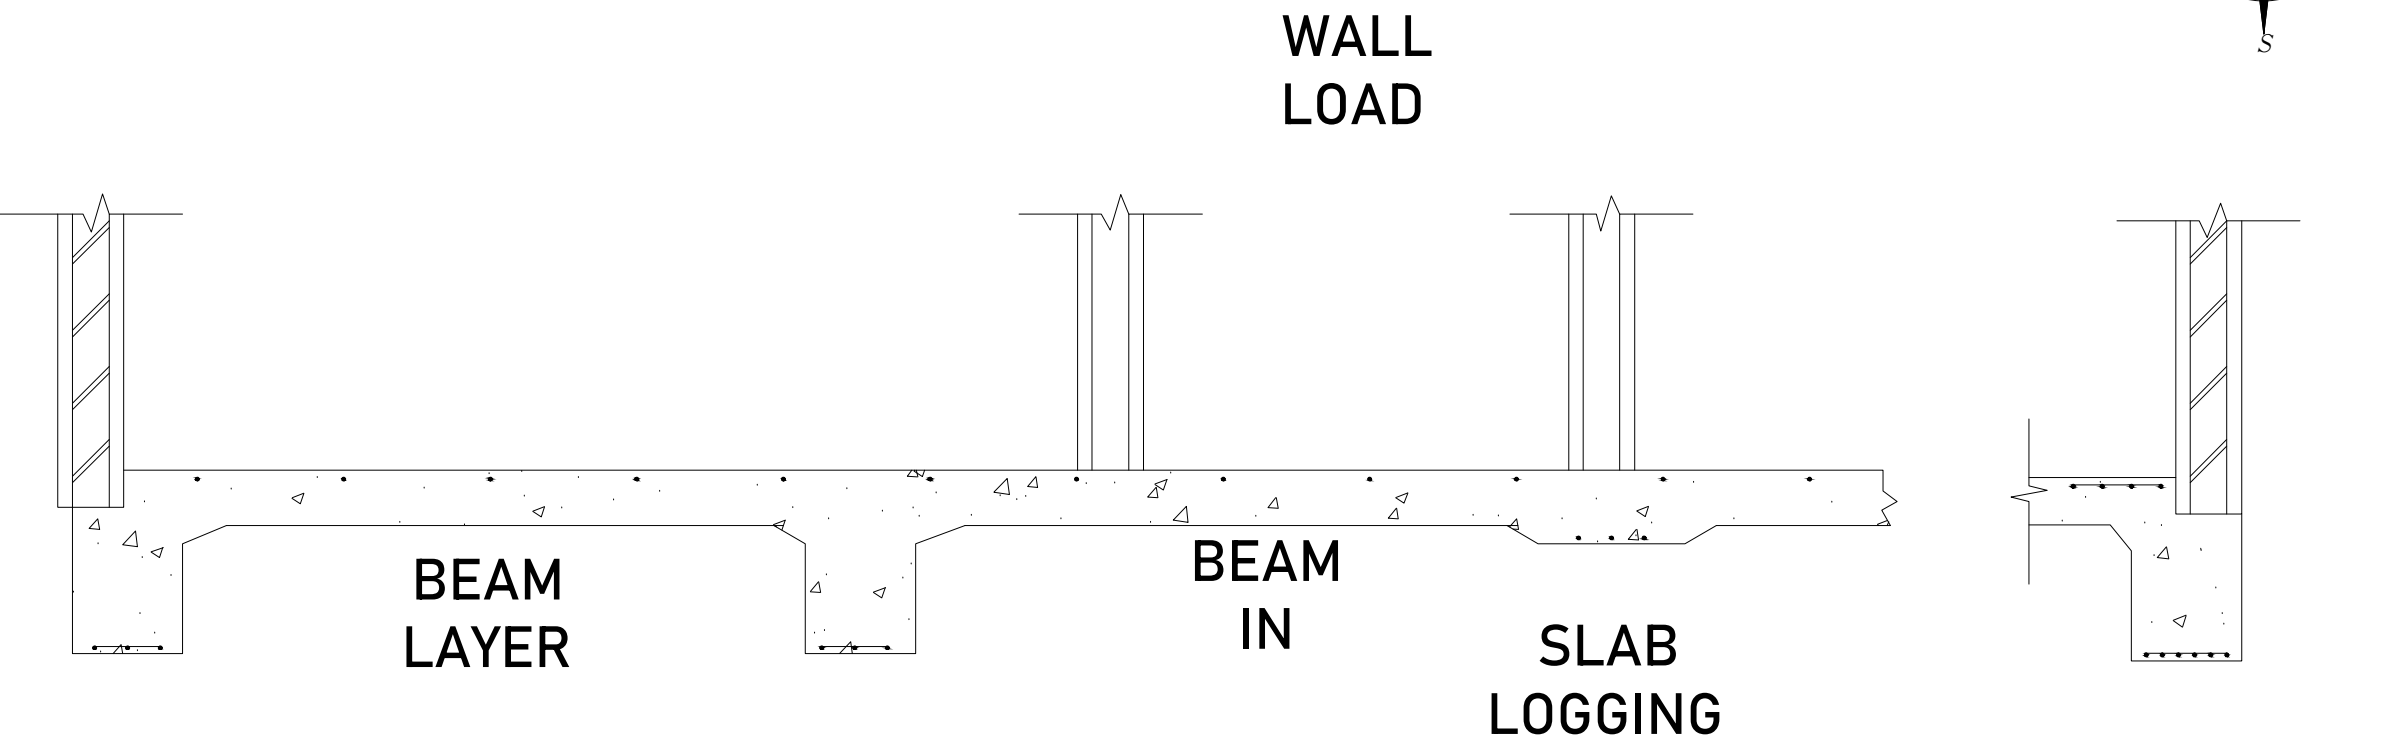

SLAB DETAIL

Scale 1 : 20

NOTE

INSTITUTION



FACULTY OF ENGINEERING
UNIVERSITY SWADAYA GUNUNG
JATI CIREBON

TASK NAME

FINAL SEMESTER ASSIGNMENT

PROFESSION PLANNING
AND DESIGN
HIGH RISE BUILDING

MADE AS A FINAL SEMESTER
EXAMINATION ASSIGNMENT SCHOOL
YEAR 2020

LECTURER

INITIALS

Dr. SAIHUL ANWAR,Ir., M.Eng., MM.
NIDN. 417085401

DRAWN BY

INITIALS

MUHAMMAD NAZMI F
NPM. 120130085



IMAGE TITLE

HOTEL BUILDING
PLANNING WORK

IMAGE NAME

SLAB DETAIL

DATE	SCALE	DRAWING NUMBER	REVISION
03 FEBUARY 2021	1 : 20	21	-

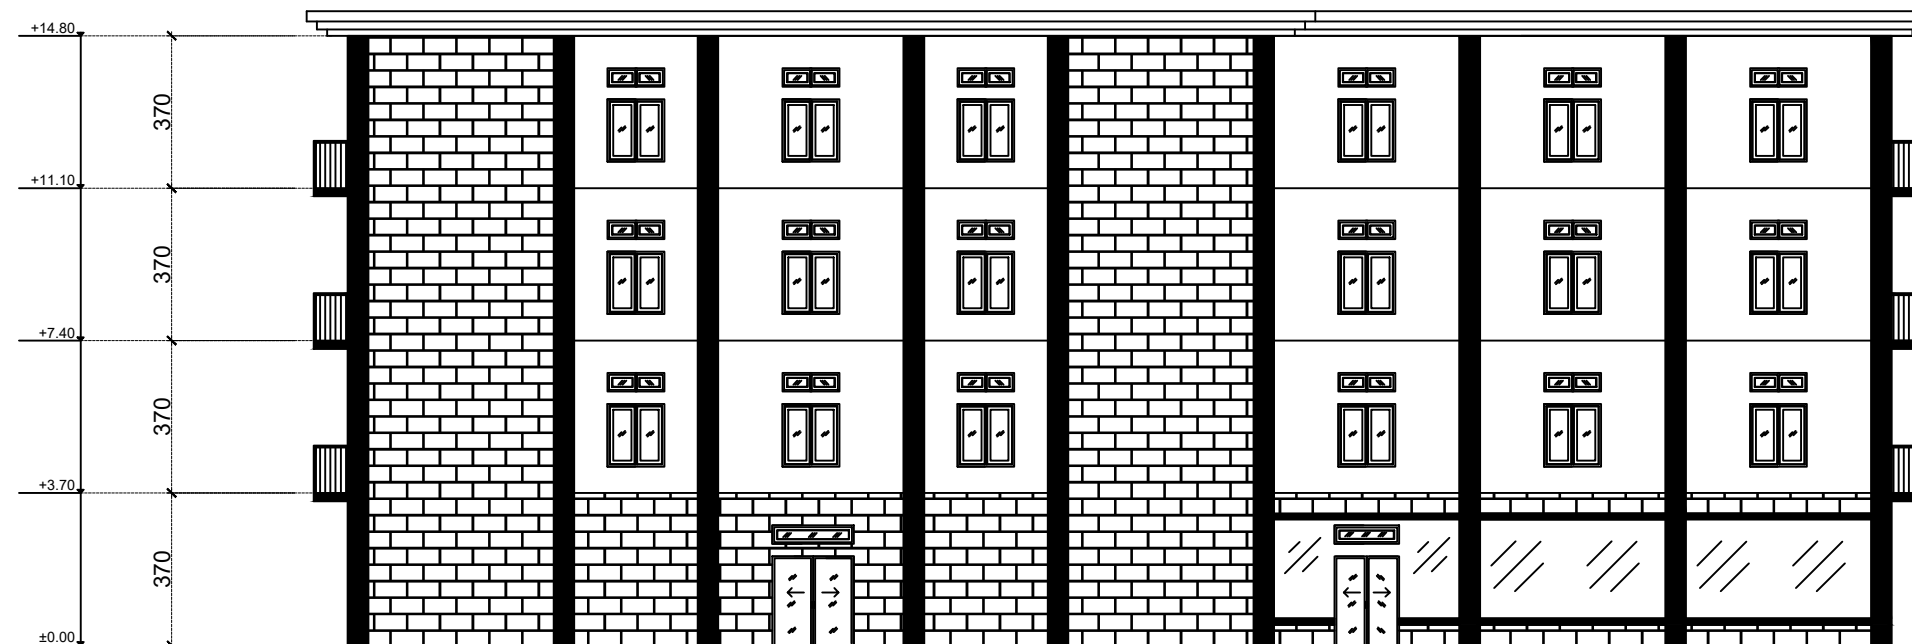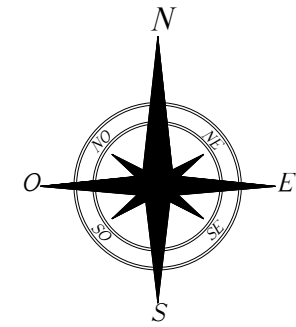

VIEW FROM THE FRONT

Skala 1 : 100

NOTE

INSTITUTION



FACULTY OF ENGINEERING
UNIVERSITY SWADAYA GUNUNG
JATI CIREBON

TASK NAME

FINAL SEMESTER ASSIGNMENT

PROFESSION PLANNING
AND DESIGN
HIGH RISE BUILDING

MADE AS A FINAL SEMESTER
EXAMINATION ASSIGNMENT SCHOOL
YEAR 2020

LECTURER

Dr. SAIHUL ANWAR,Ir., M.Eng., MM.
NIDN. 417085401

INITIALS

DRAWN BY

MUHAMMAD NAZMI F
NPM. 120130085

INITIALS



IMAGE TITLE

HOTEL BUILDING
PLANNING WORK

IMAGE NAME

VIEW FROM THE FRONT

DATE	SCALE	DRAWING NUMBER	REVISION
03 FEBUARY 2021	1 : 100	22	-

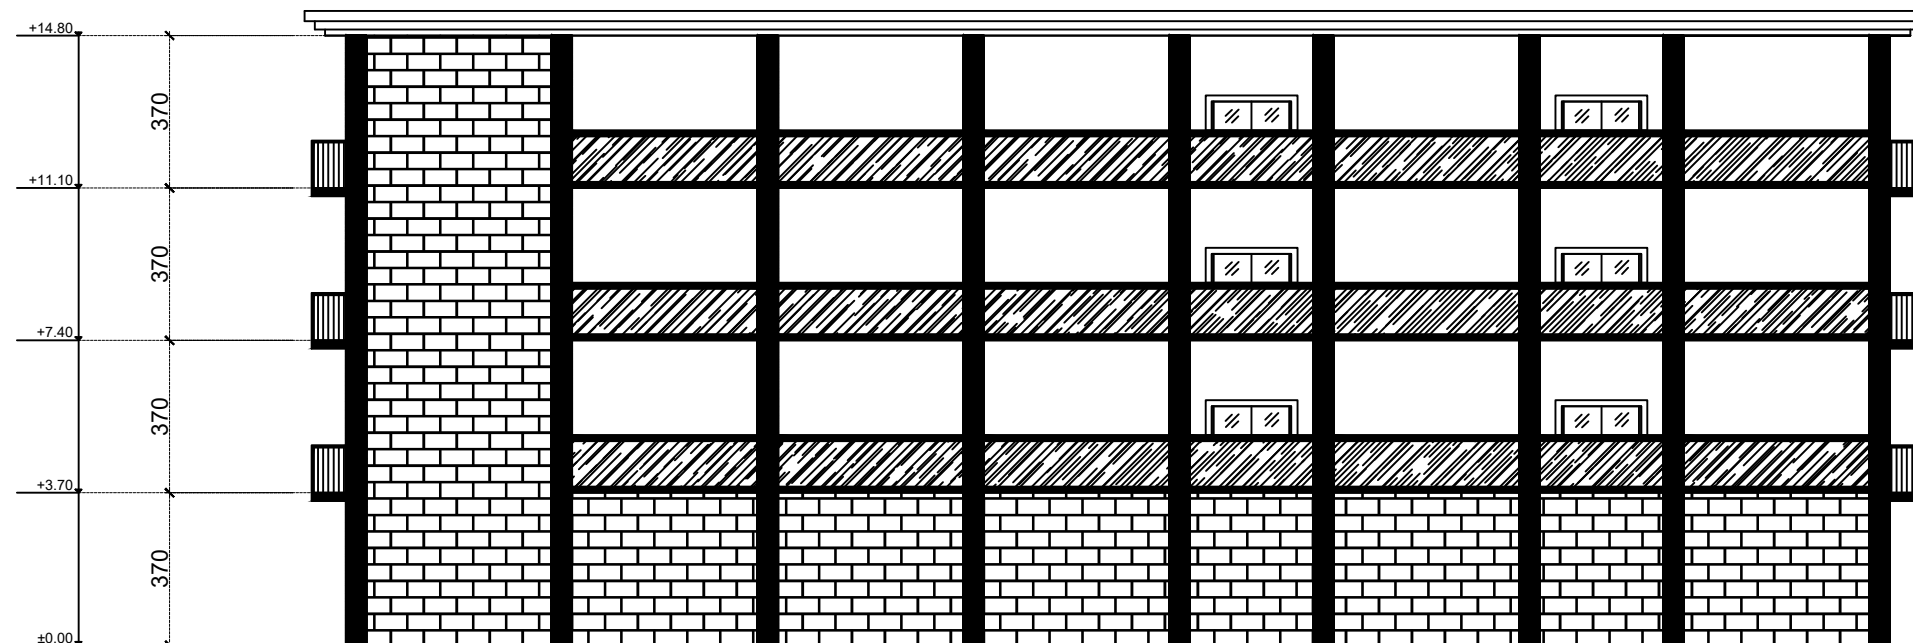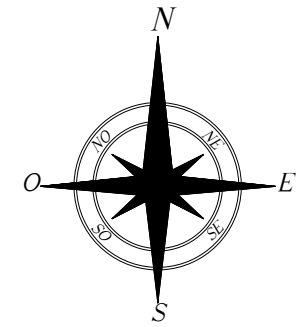

BACK VIEW
Skala 1 : 100

NOTE

INSTITUTION



FACULTY OF ENGINEERING
UNIVERSITY SWADAYA GUNUNG
JATI CIREBON

TASK NAME

FINAL SEMESTER ASSIGNMENT

PROFESSION PLANNING
AND DESIGN
HIGH RISE BUILDING

MADE AS A FINAL SEMESTER
EXAMINATION ASSIGNMENT SCHOOL
YEAR 2020

LECTURER

Dr. SAIHUL ANWAR,Ir., M.Eng., MM.
NIDN. 417085401

INITIALS

DRAWN BY

MUHAMMAD NAZMI F
NPM. 120130085

INITIALS



IMAGE TITLE

HOTEL BUILDING
PLANNING WORK

IMAGE NAME

BACK VIEW

DATE	SCALE	DRAWING NUMBER	REVISION
03 FEBUARY 2021	1 : 100	23	-

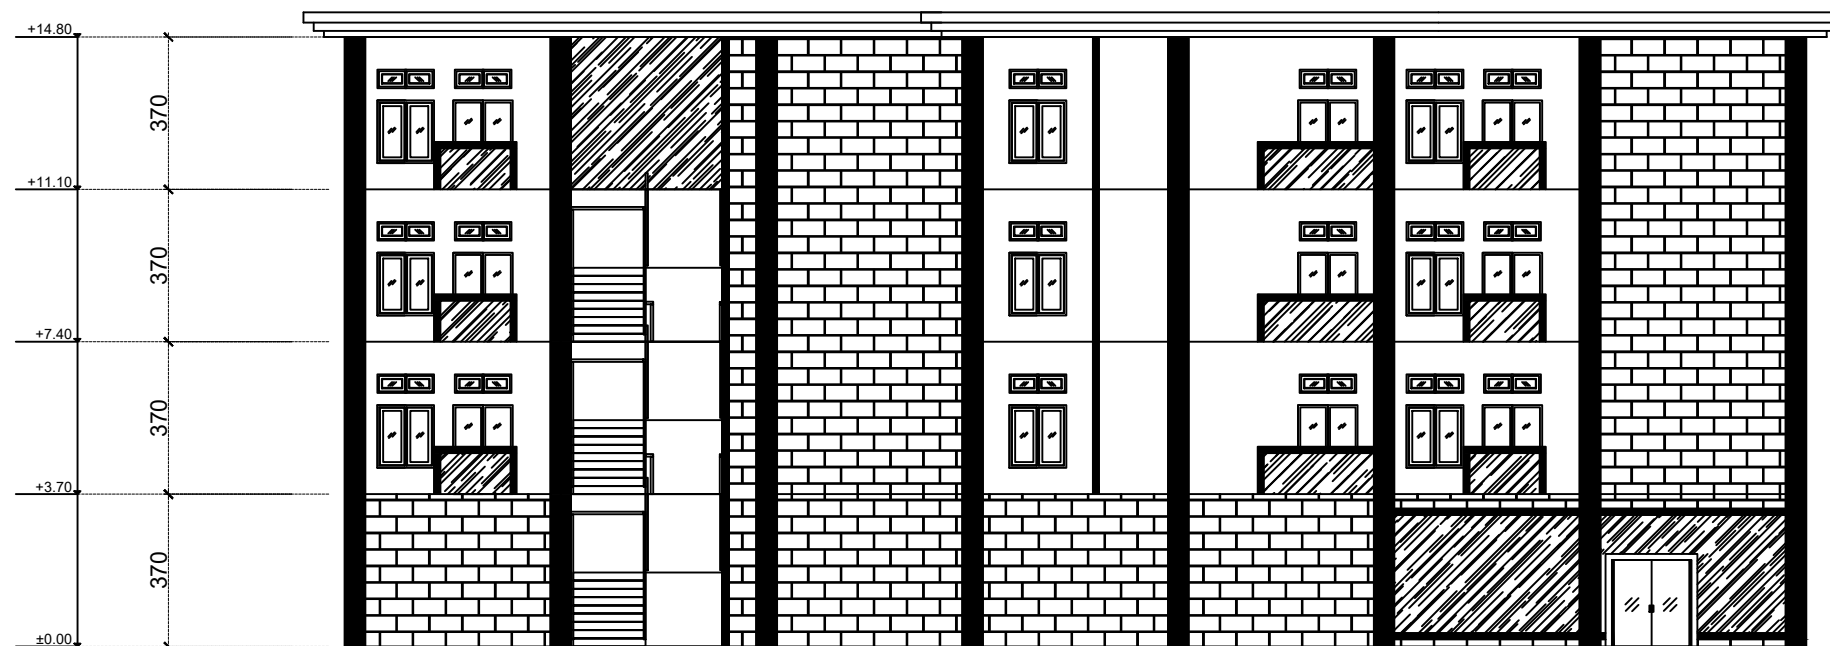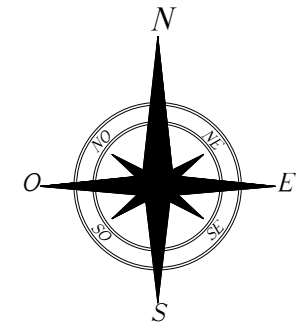

RIGHT SIDE VIEW

Skala 1 : 100

NOTE

INSTITUTION



FACULTY OF ENGINEERING
UNIVERSITY SWADAYA GUNUNG
JATI CIREBON

TASK NAME

FINAL SEMESTER ASSIGNMENT

PROFESSION PLANNING
AND DESIGN
HIGH RISE BUILDING

MADE AS A FINAL SEMESTER
EXAMINATION ASSIGNMENT SCHOOL
YEAR 2020

LECTURER

INITIALS

Dr. SAIHUL ANWAR,Ir., M.Eng., MM.
NIDN. 417085401

DRAWN BY

INITIALS

MUHAMMAD NAZMI F
NPM. 120130085

IMAGE TITLE

HOTEL BUILDING
PLANNING WORK

IMAGE NAME

RIGHT SIDE VIEW

DATE

SCALE

DRAWING
NUMBER


REVISION

03
FEBUARY
2021

1 : 100

24

-

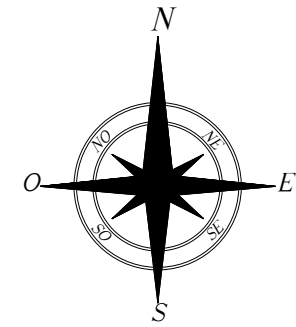

LEFT SIDE VIEW

Skala 1 : 100

NOTE

INSTITUTION



FACULTY OF ENGINEERING
UNIVERSITY SWADAYA GUNUNG
JATI CIREBON

TASK NAME

FINAL SEMESTER ASSIGNMENT

PROFESSION PLANNING
AND DESIGN
HIGH RISE BUILDING

MADE AS A FINAL SEMESTER
EXAMINATION ASSIGNMENT SCHOOL
YEAR 2020

LECTURER

INITIALS

Dr. SAIHUL ANWAR,Ir., M.Eng., MM.
NIDN. 417085401

DRAWN BY

INITIALS

MUHAMMAD NAZMI F
NPM. 120130085

IMAGE TITLE

HOTEL BUILDING
PLANNING WORK

IMAGE NAME

LEFT SIDE VIEW

DATE	SCALE	DRAWING NUMBER	REVISION
03 FEBUARY 2021	1 : 100	25	-