


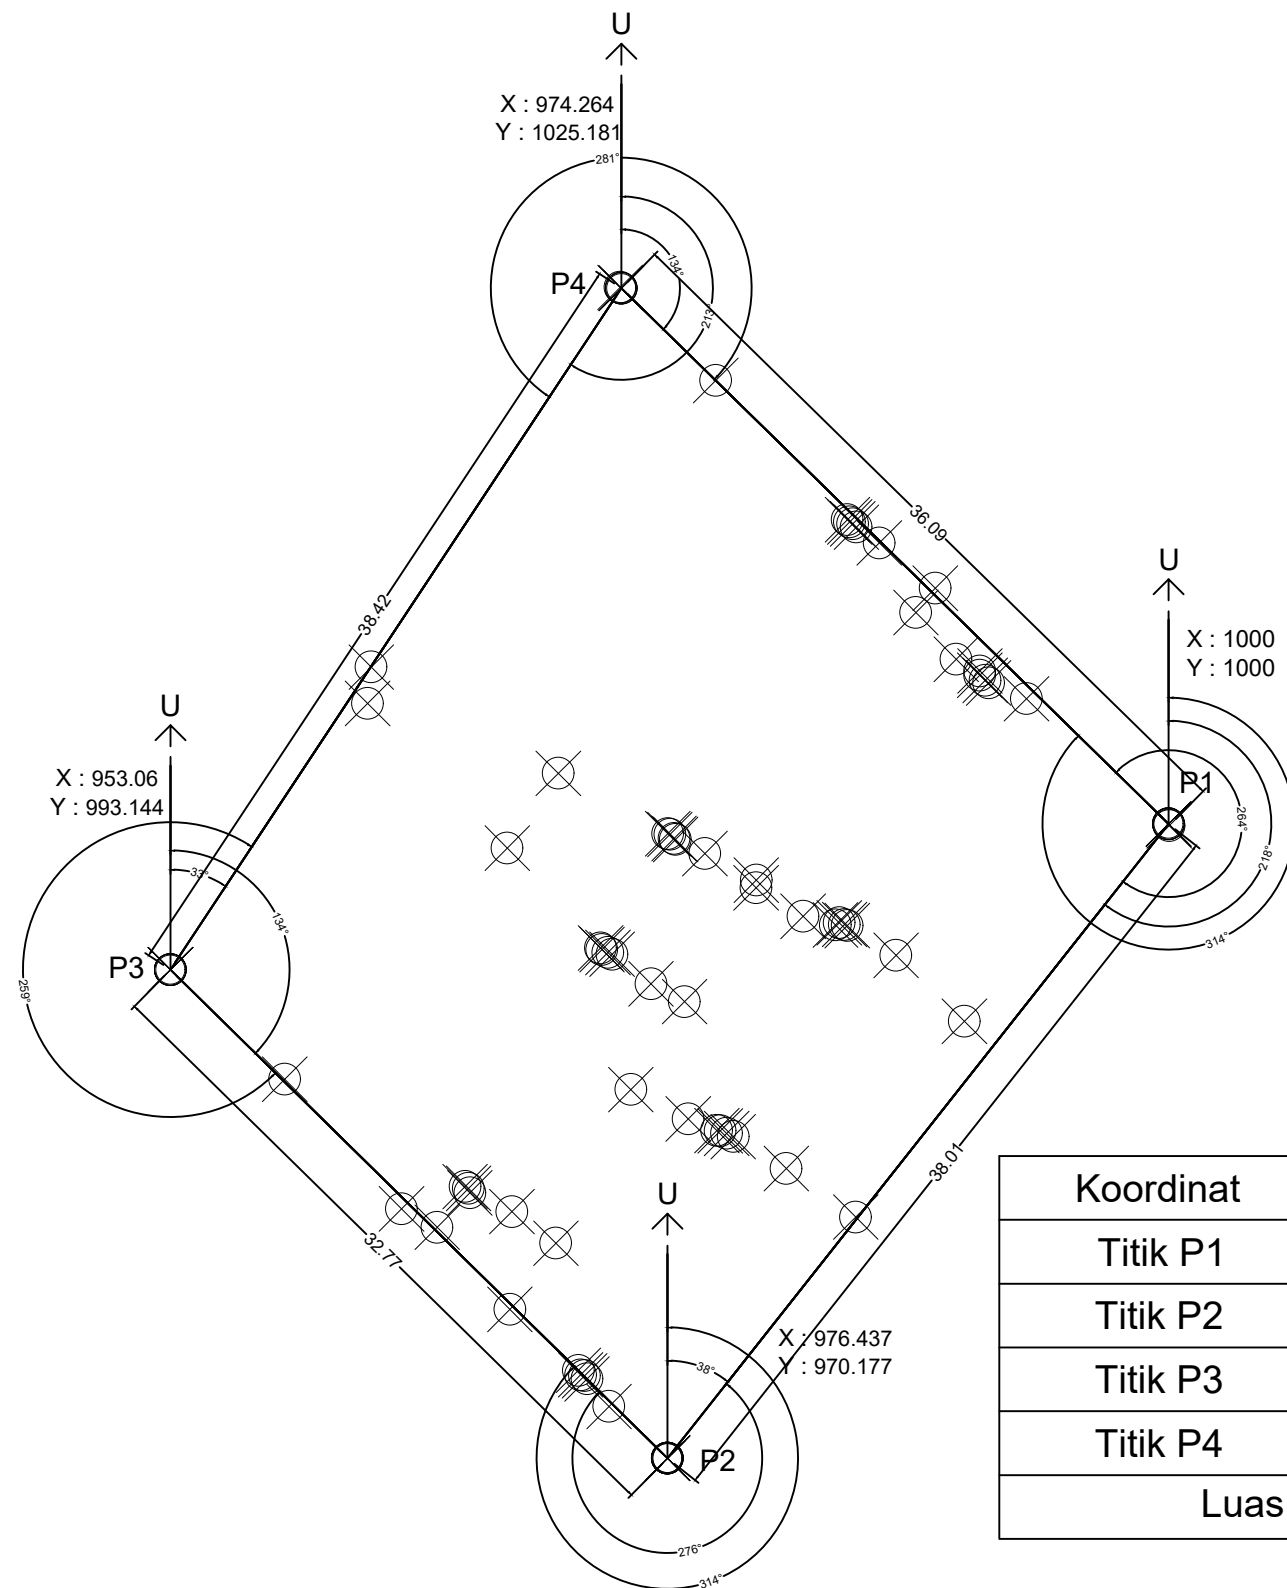

INSTANSI

UNIVERSITAS SWADAYA
GUNUNG JATI
CIREBON

JUDUL GAMBAR

LAMPIRAN LAPRAK IUT 2

NAMA GAMBAR

SKETSA POLIGON
TERTUTUP

DIHITUNG/DIGAMBAR

KELOMPOK 4A

1. BRAMUDYA GUSTI
(120130009)
2. FAZLUR RAHMAN
(120130034)
3. ADZ DZYIKRI
(120130040)
4. MUHAMMAD NAZMI F
(120130085)
5. TRI ARDIANSYAH
(120130195)
6. GITTA KARINA
(120130156)

DISETUJUI

DOSEN IUT 2
H. Awliya Tribhuwana, S.T.,MT

Asdos Praktikum IUT 2
Muhammad Hilman Rodifa

TANGGAL PRAKTIKUM

16 APRIL 2022


SKALA

1 : 400

SATUAN

M

CATATAN

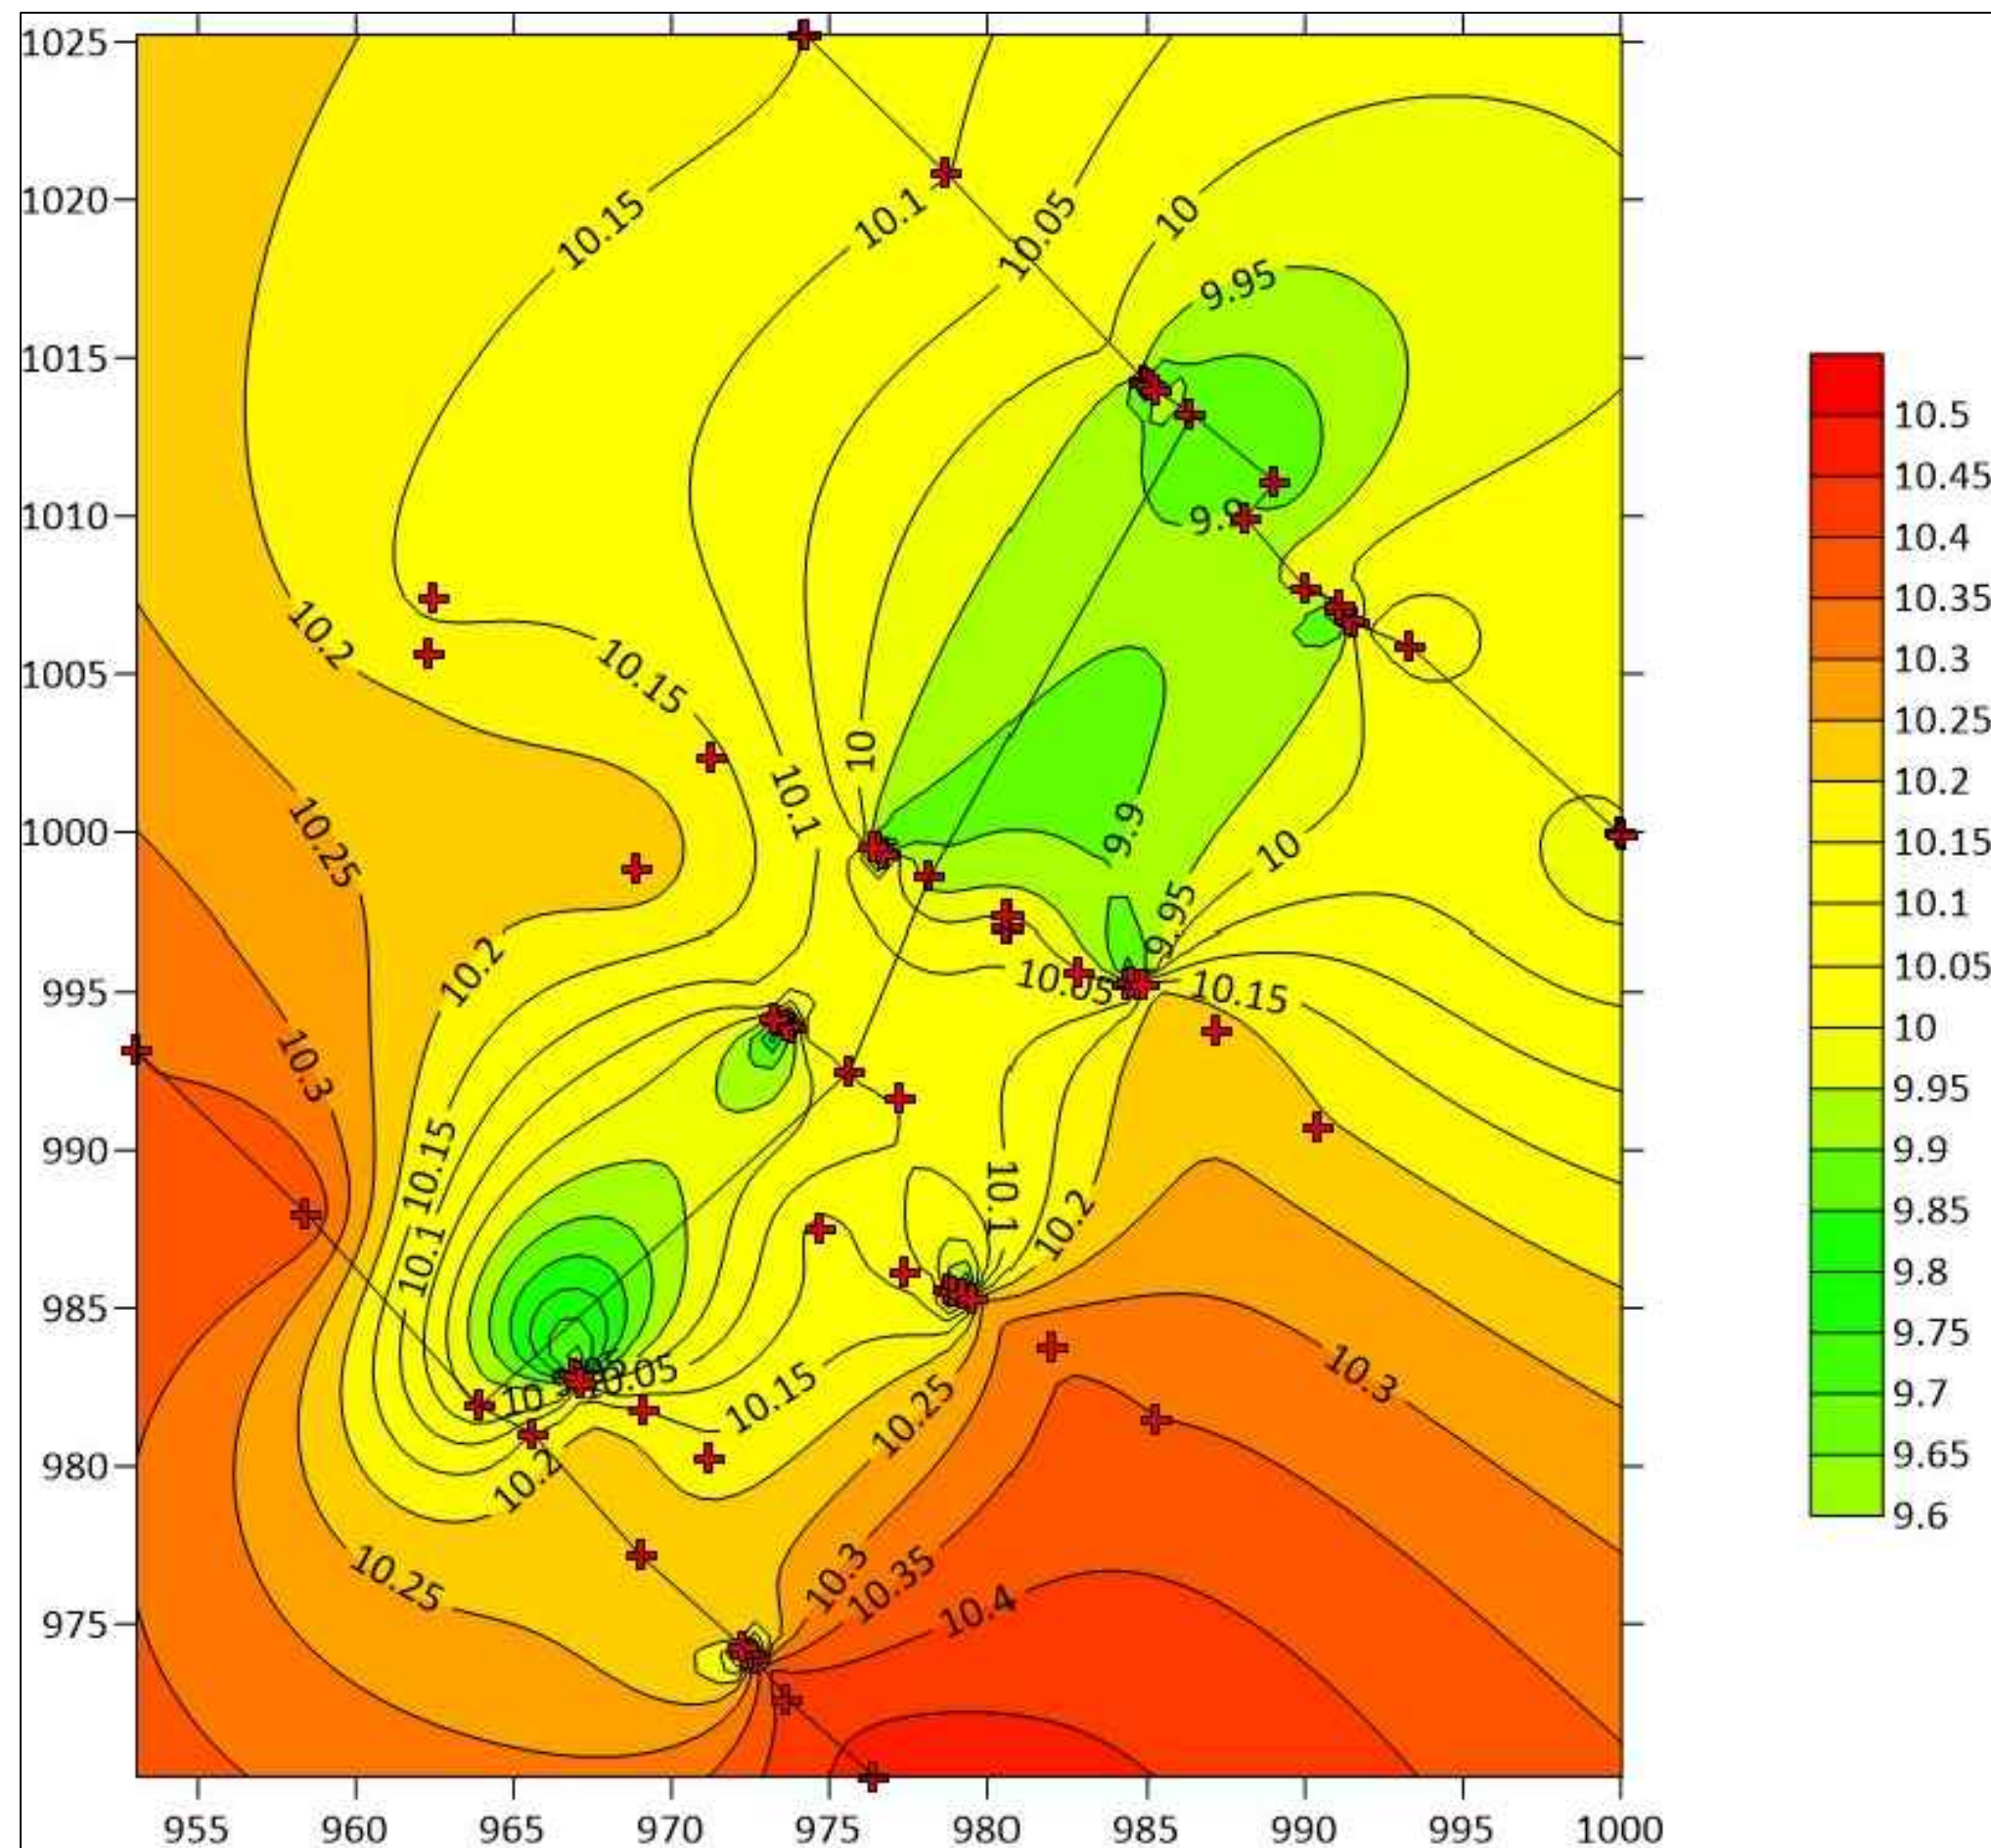

INSTANSI

UNIVERSITAS SWADAYA
GUNUNG JATI
CIREBON

JUDUL GAMBAR

LAMPIRAN LAPRAK IUT 2

NAMA GAMBAR

SKETSA KONTUR 2D

DIHITUNG/DIGAMBAR

KELOMPOK 4A

1. BRAMUDYA GUSTI
(120130009)
2. FAZLUR RAHMAN
(120130034)
3. ADZ DZYIKRI
(120130040)
4. MUHAMMAD NAZMI F
(120130085)
5. TRI ARDIANSYAH
(120130195)
6. GITTA KARINA
(120130156)

DISETUJUI

DOSEN IUT 2
H. Awliya Tribhuwana, S.T.,MT

Asdos Praktikum IUT 2
Muhammad Hilman Rodifa

TANGGAL PRAKTIKUM

16 APRIL 2022


SKALA

SATUAN

1 : 200

M

CATATAN

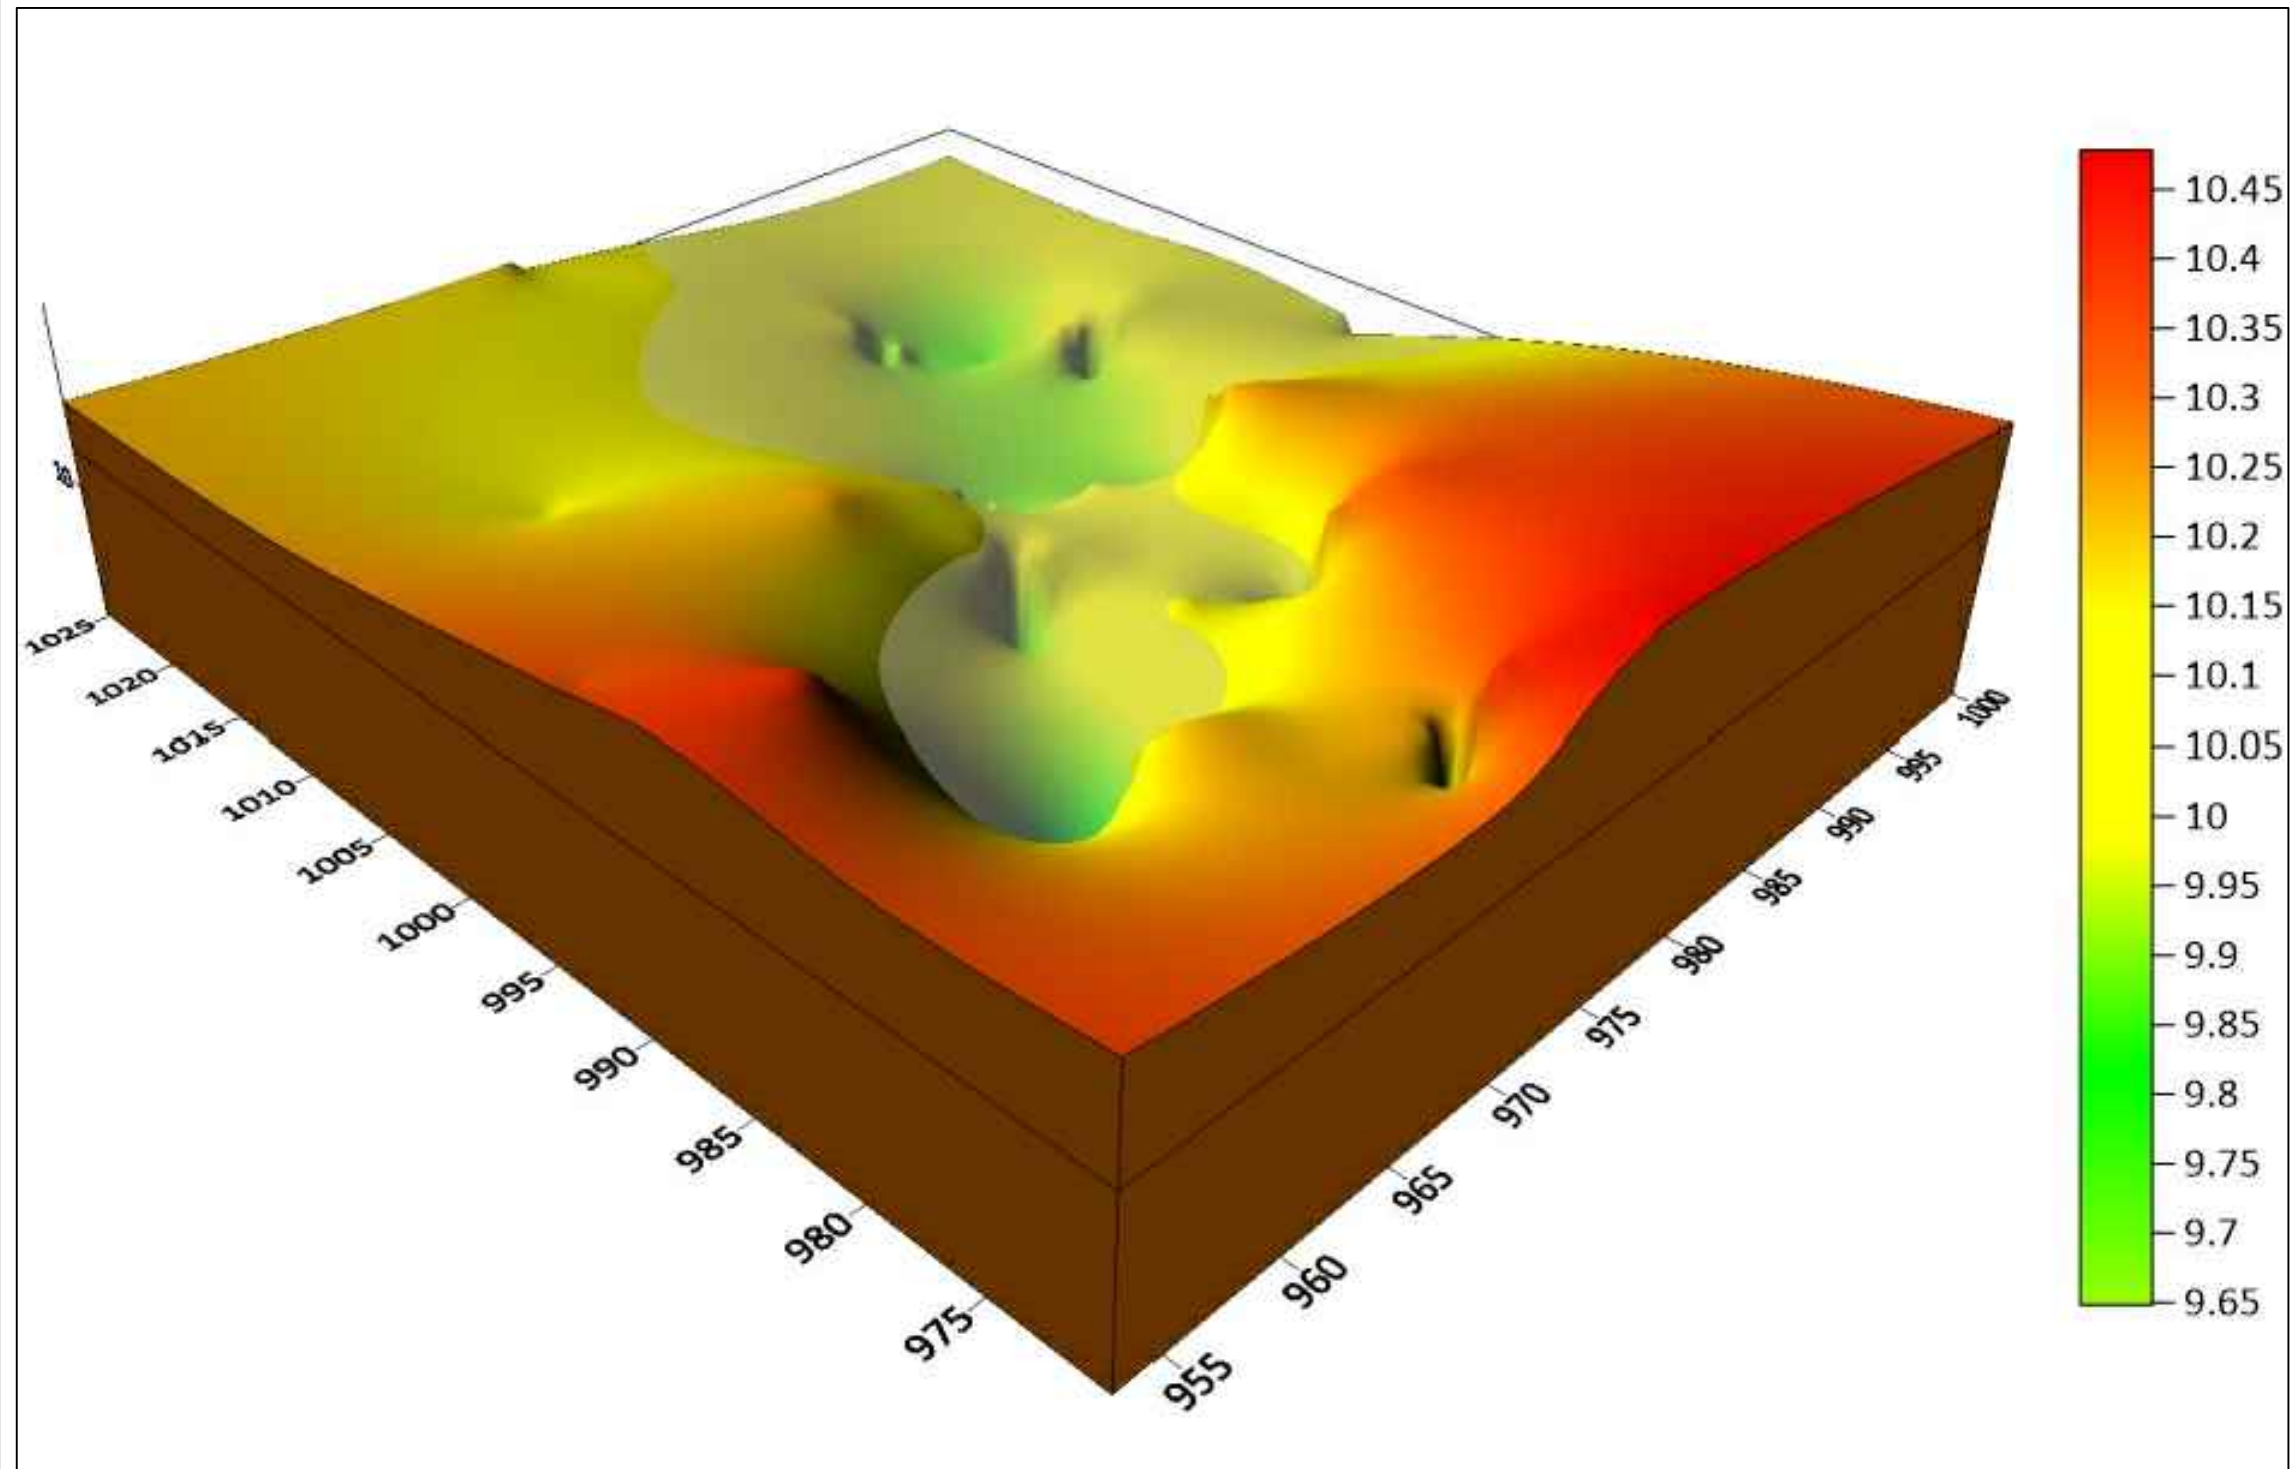

INSTANSI

UNIVERSITAS SWADAYA
GUNUNG JATI
CIREBON

JUDUL GAMBAR

LAMPIRAN LAPRAK IUT 2

NAMA GAMBAR

SKETSA 3D SURFACE

DIHITUNG/DIGAMBAR

KELOMPOK 4A

1. BRAMUDYA GUSTI
(120130009)
2. FAZLUR RAHMAN
(120130034)
3. ADZ DZYIKRI
(120130040)
4. MUHAMMAD NAZMI F
(120130085)
5. TRI ARDIANSYAH
(120130195)
6. GITTA KARINA
(120130156)

DISETUJUI

DOSEN IUT 2
H. Awliya Tribhuwana, S.T.,MT

Asdos Praktikum IUT 2
Muhammad Hilman Rodifa

TANGGAL PRAKTIKUM

16 APRIL 2022


SKALA

1 : 200

SATUAN

M

CATATAN

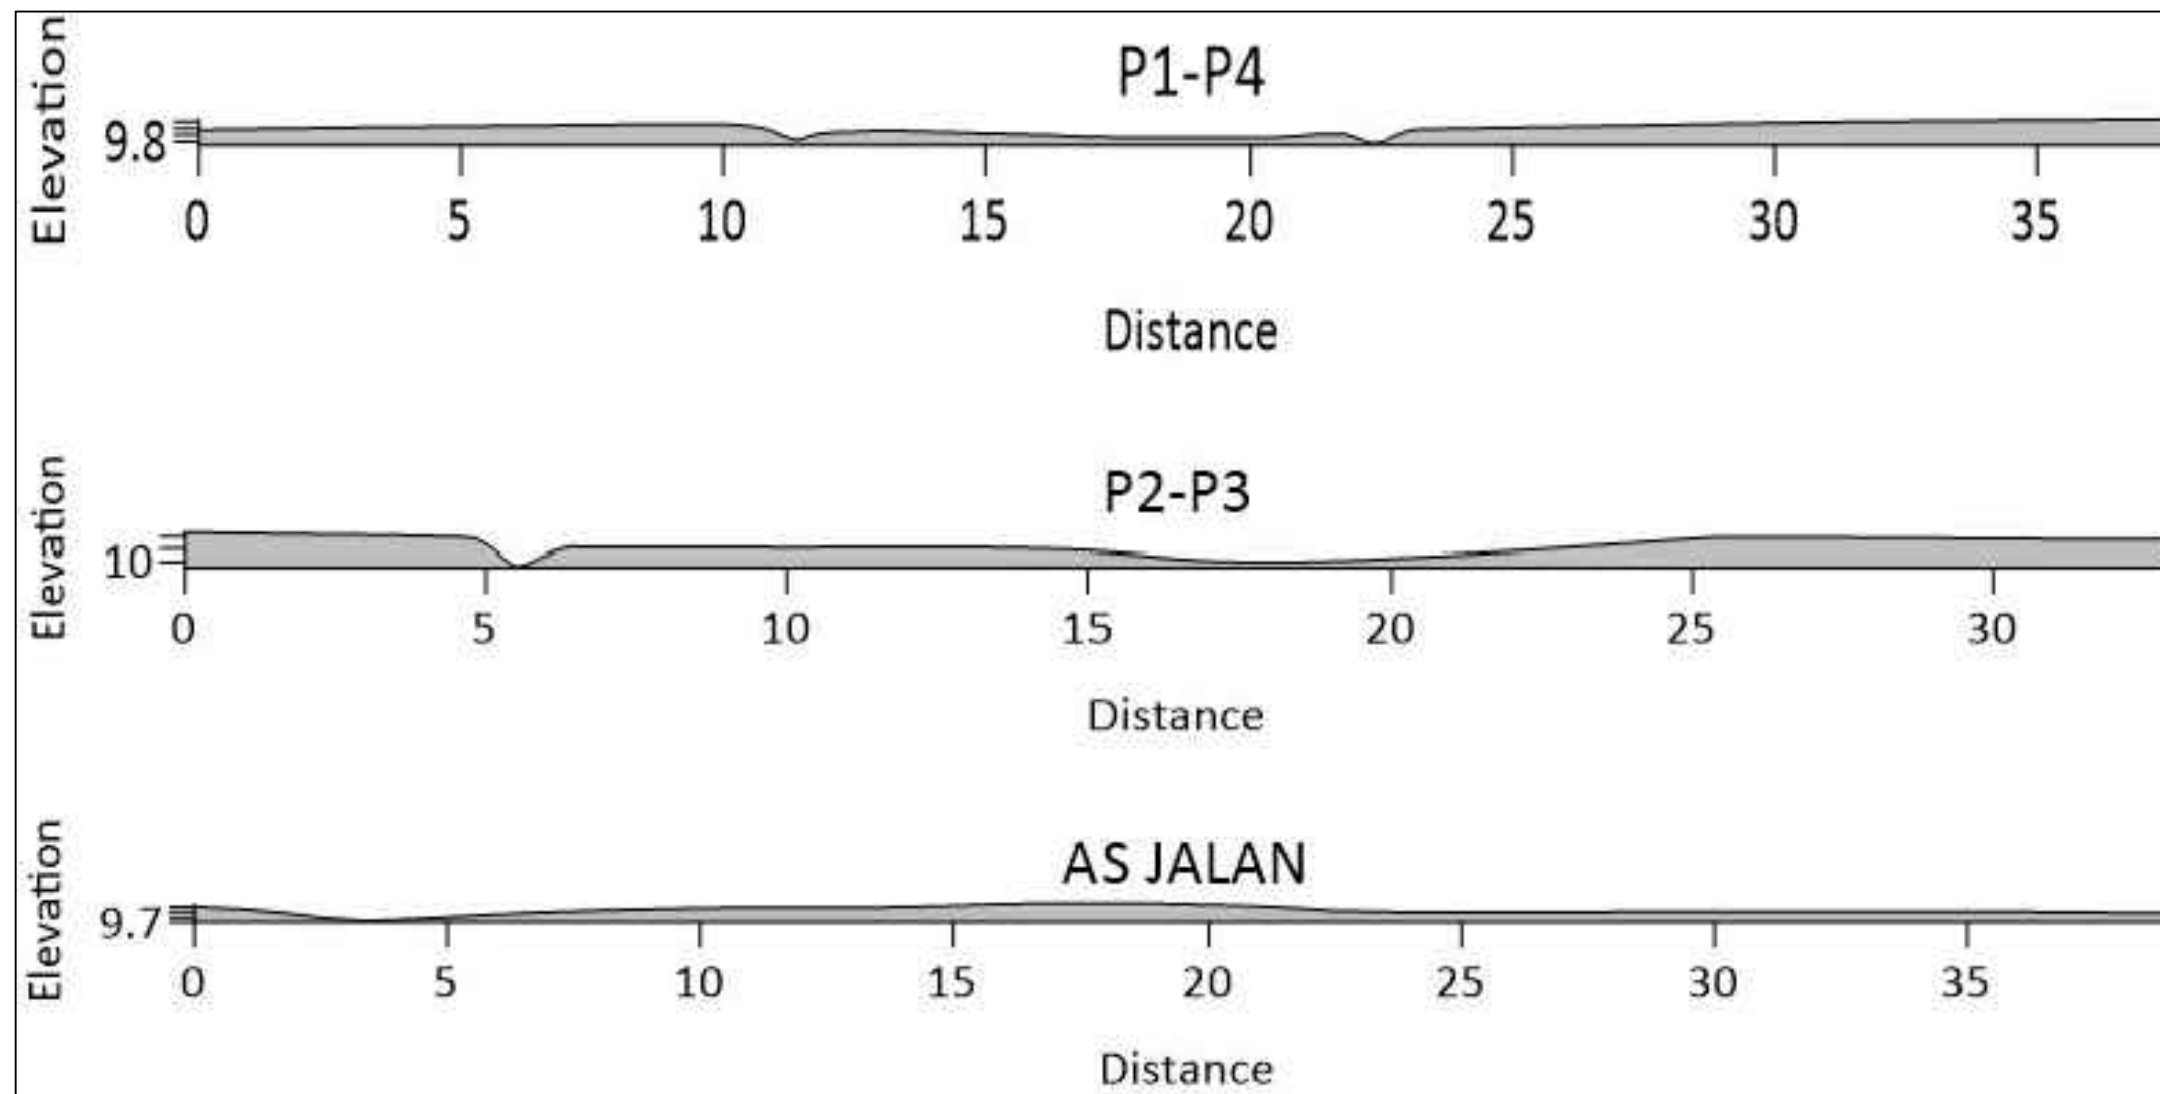

INSTANSI

UNIVERSITAS SWADAYA
GUNUNG JATI
CIREBON

JUDUL GAMBAR

LAMPIRAN LAPRAK IUT 2

NAMA GAMBAR

GAMBAR POTONGAN

DIHITUNG/DIGAMBAR

KELOMPOK 4A

1. BRAMUDYA GUSTI
(120130009)
2. FAZLUR RAHMAN
(120130034)
3. ADZ DZYIKRI
(120130040)
4. MUHAMMAD NAZMI F
(120130085)
5. TRI ARDIANSYAH
(120130195)
6. GITTA KARINA
(120130156)

DISETUJUI

DOSEN IUT 2
H. Awliya Tribhuwana, S.T.,MT

Asdos Praktikum IUT 2
Muhammad Hilman Rodifa

TANGGAL PRAKTIKUM

16 APRIL 2022

SKALA

1 : 200

SATUAN

M

CATATAN